GRUNDRISS M 1:20

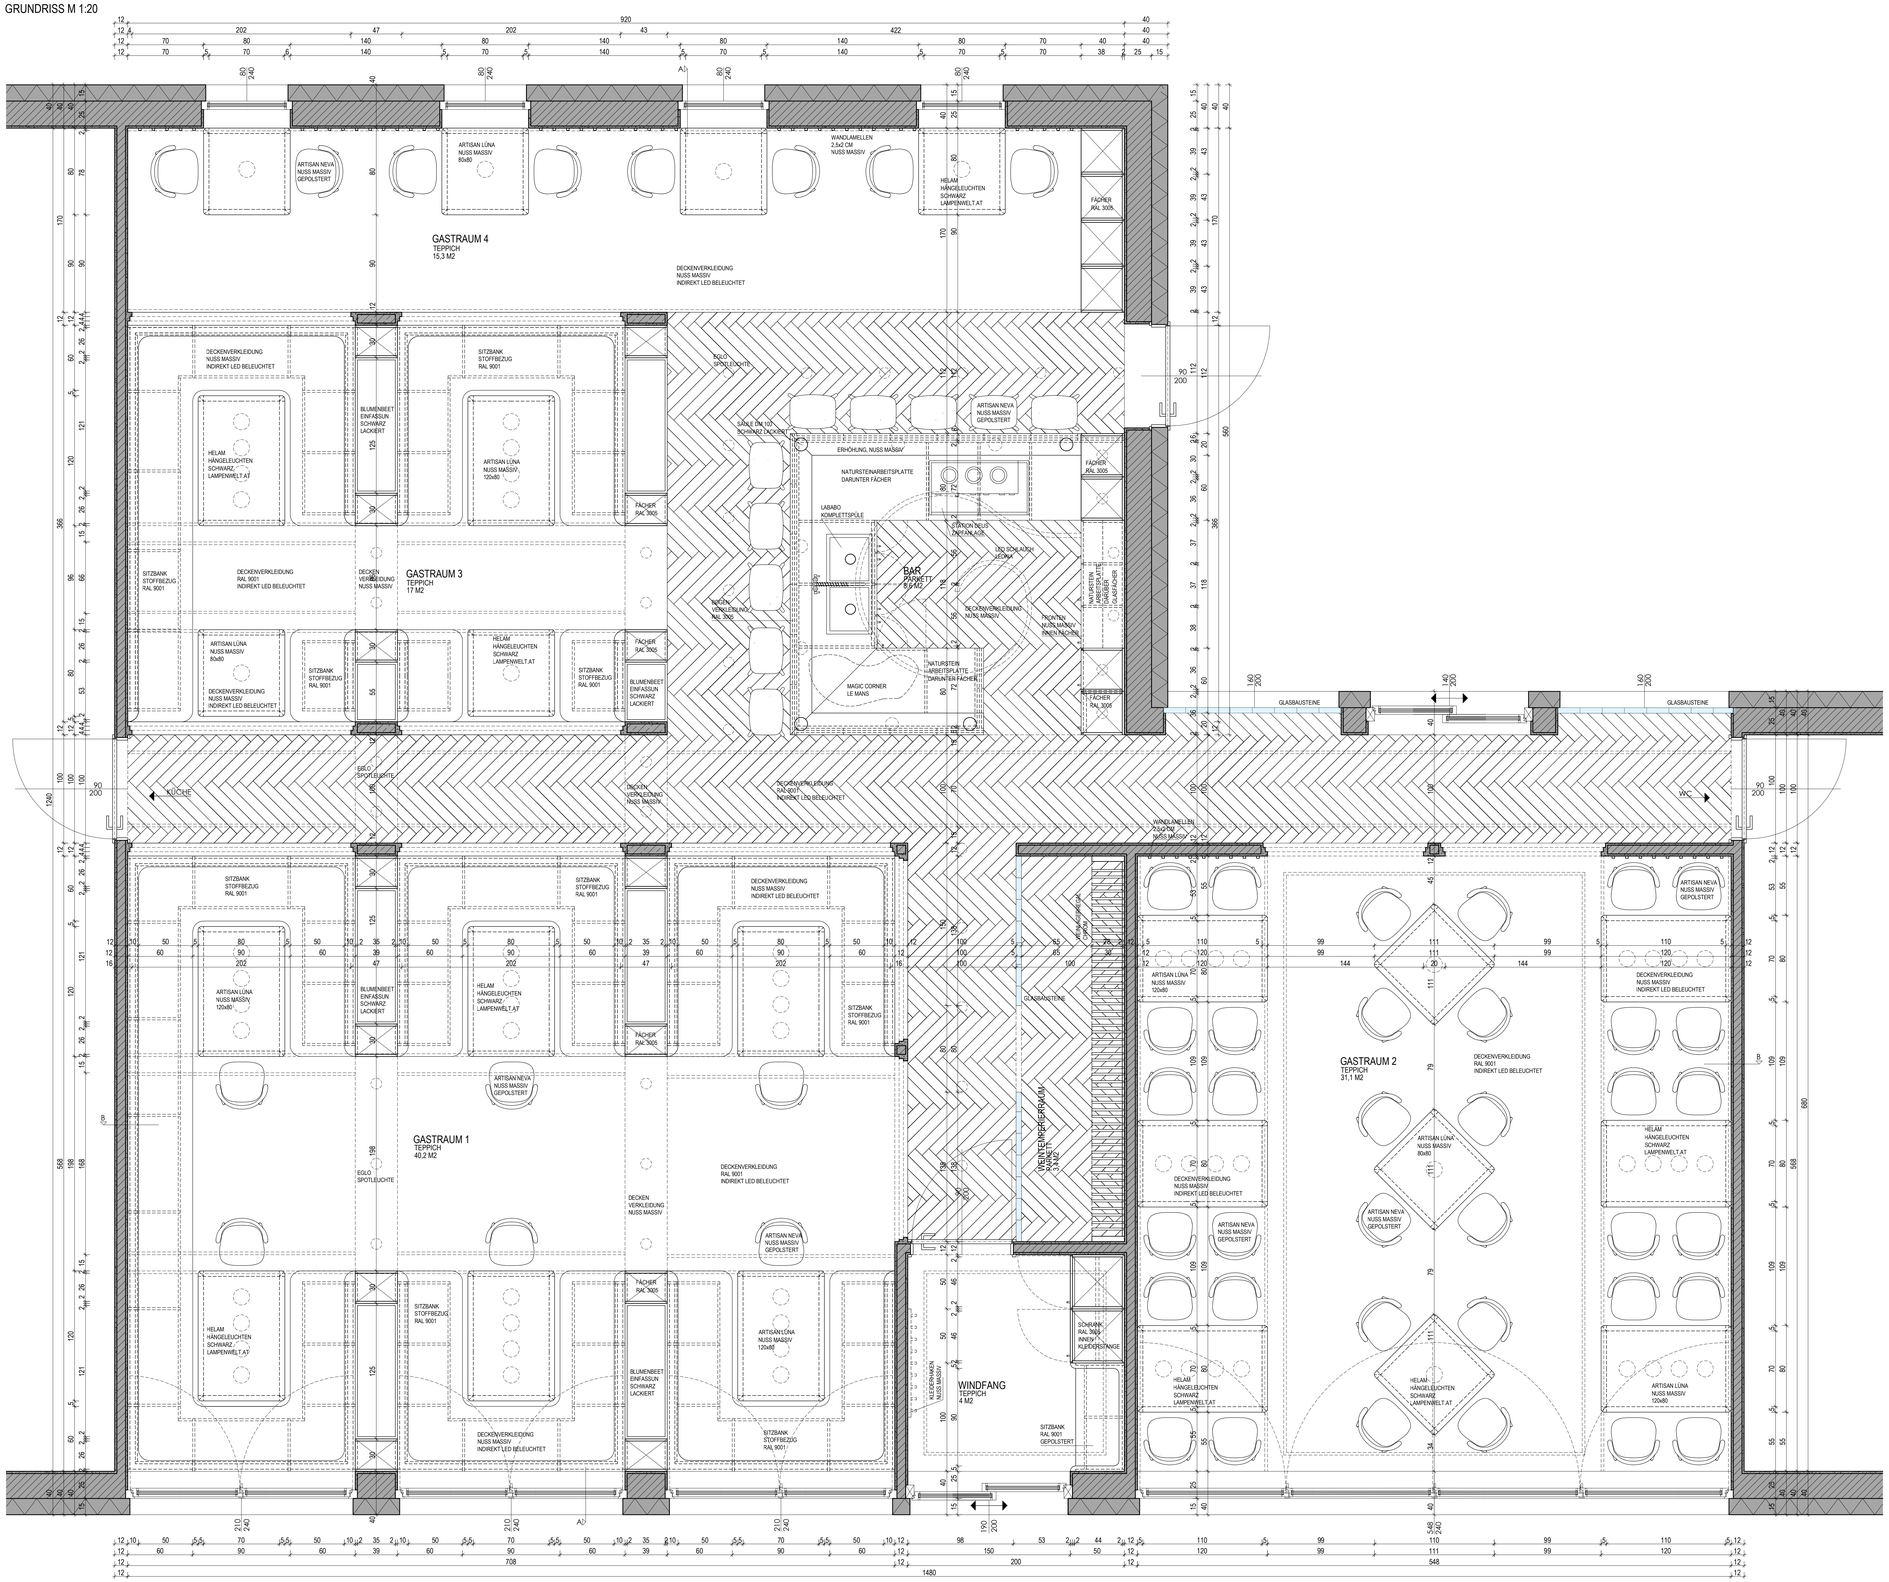

HTBLA HALLSTATT

WEINBAR BLATT 1 M 1:20 PR 3

GS-U 5yHIHR 2024/ 25 VALENTIN SCHACHINGER

ANSICHT B-B M 1:20

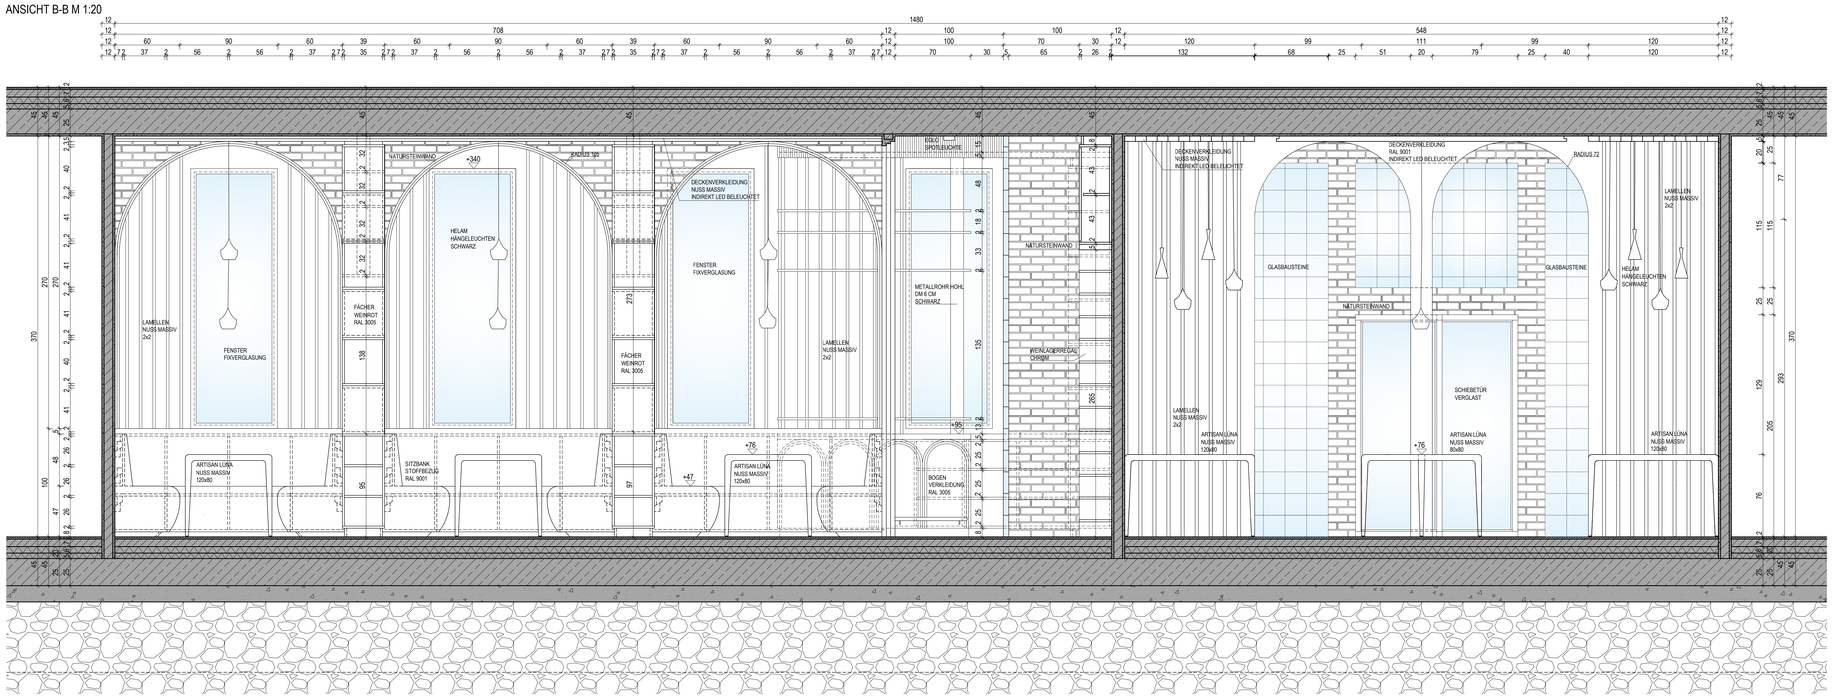

ANSICHT A-A M 1:20

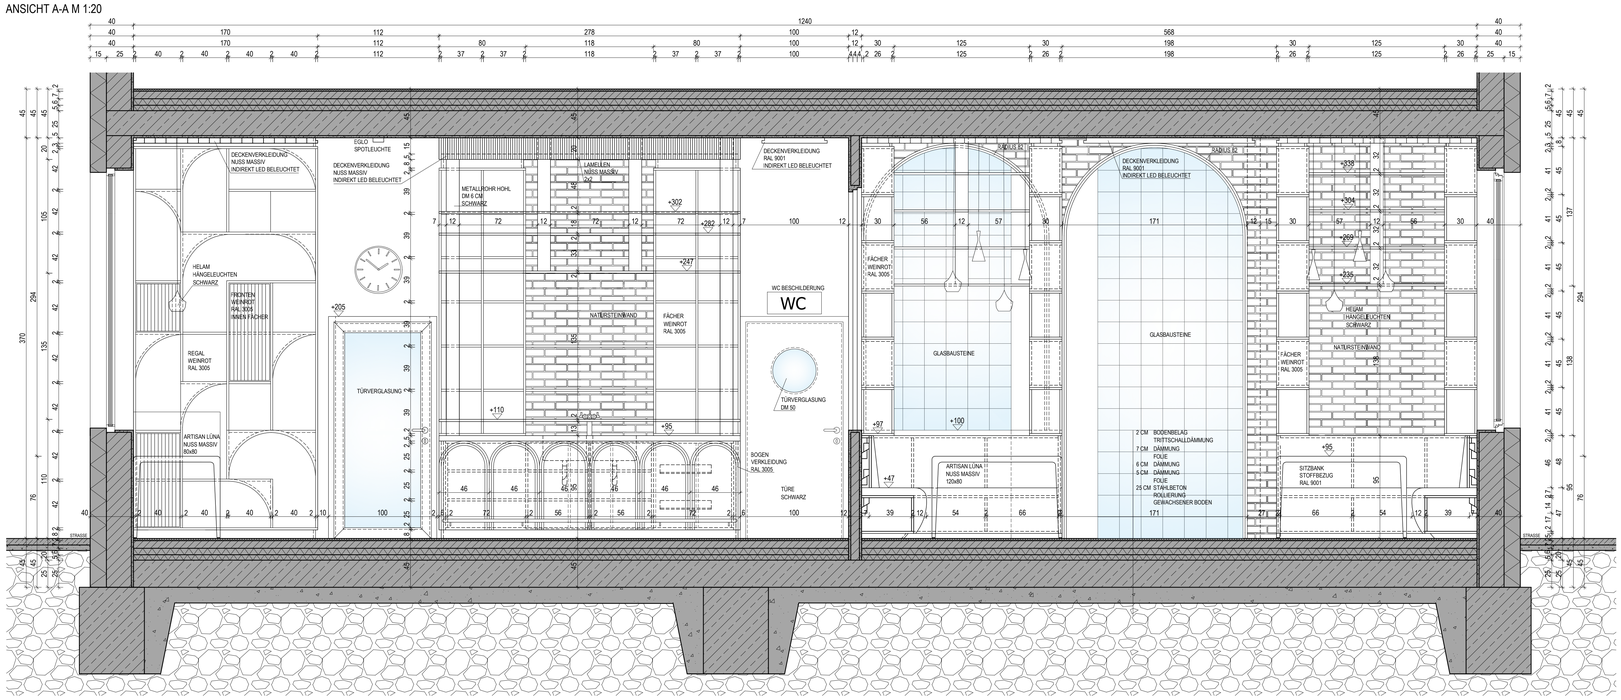

HTBLA HALLSTATT	WEINBAR	BLATT 2	M 1:20	PR 3
	GS-U 5yHIHR	2024/ 25	VALENTIN SCHACHINGER	