




ERDGESCHOSS

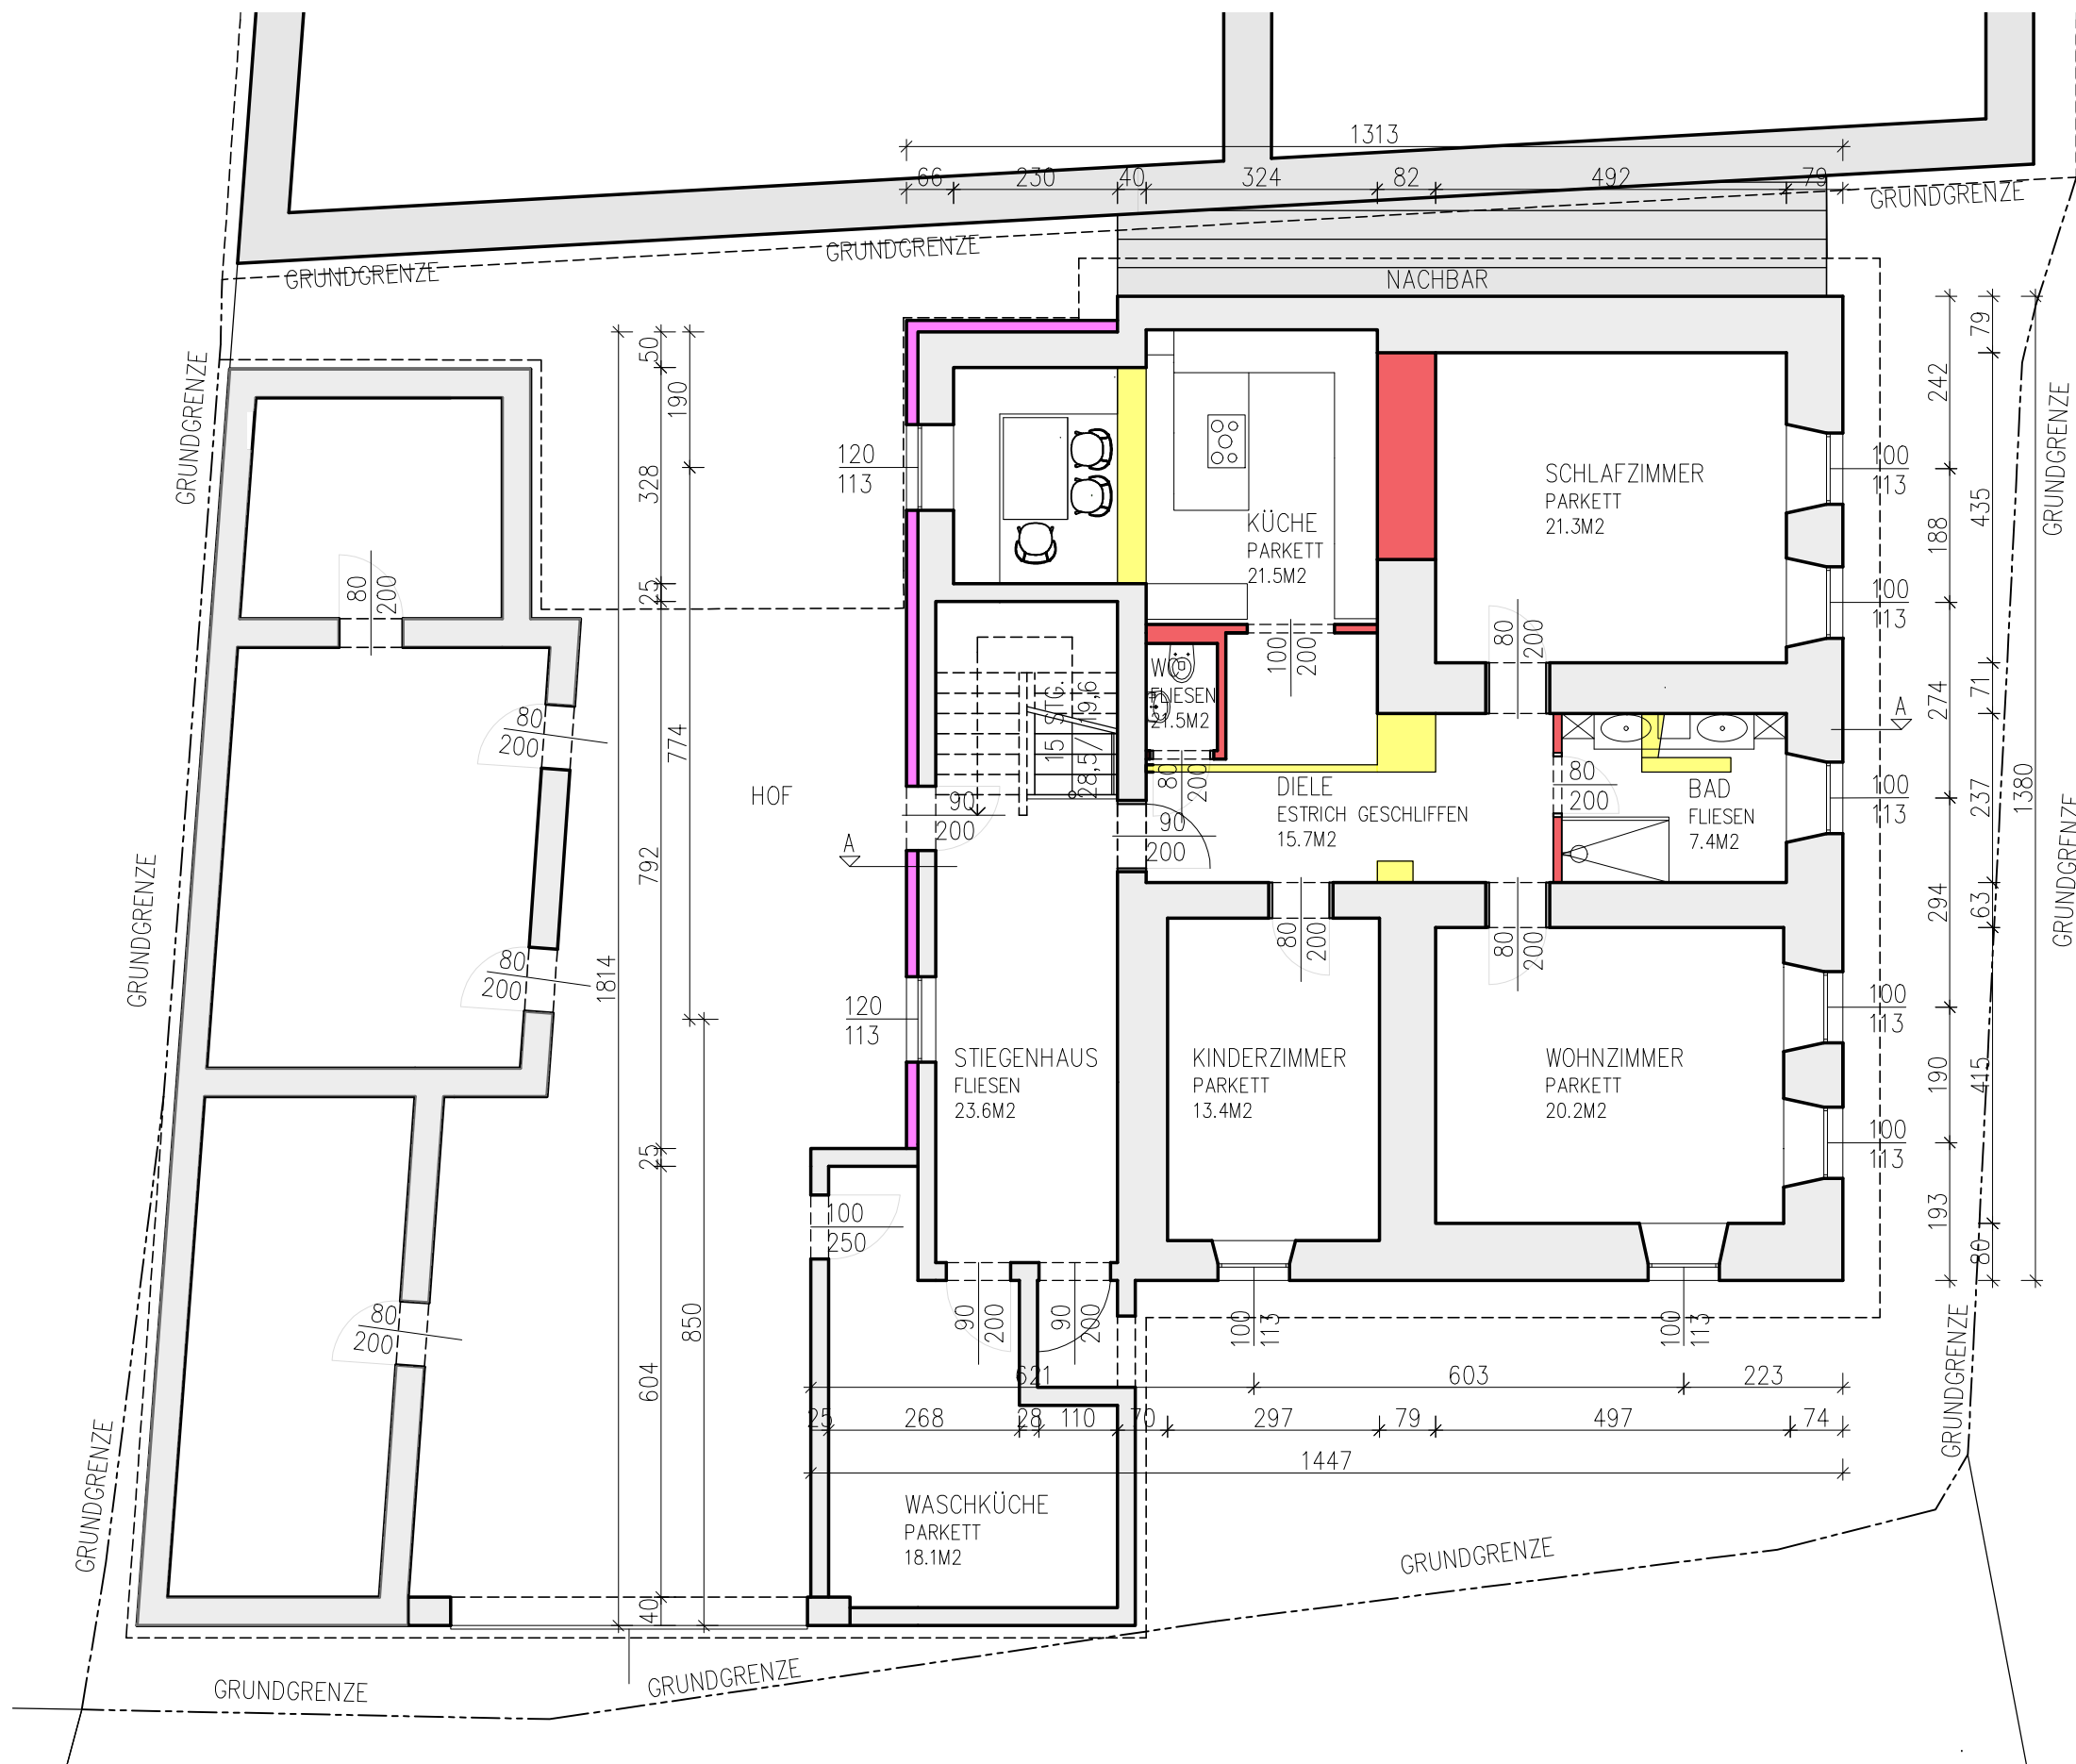



OBERGESCHOSS

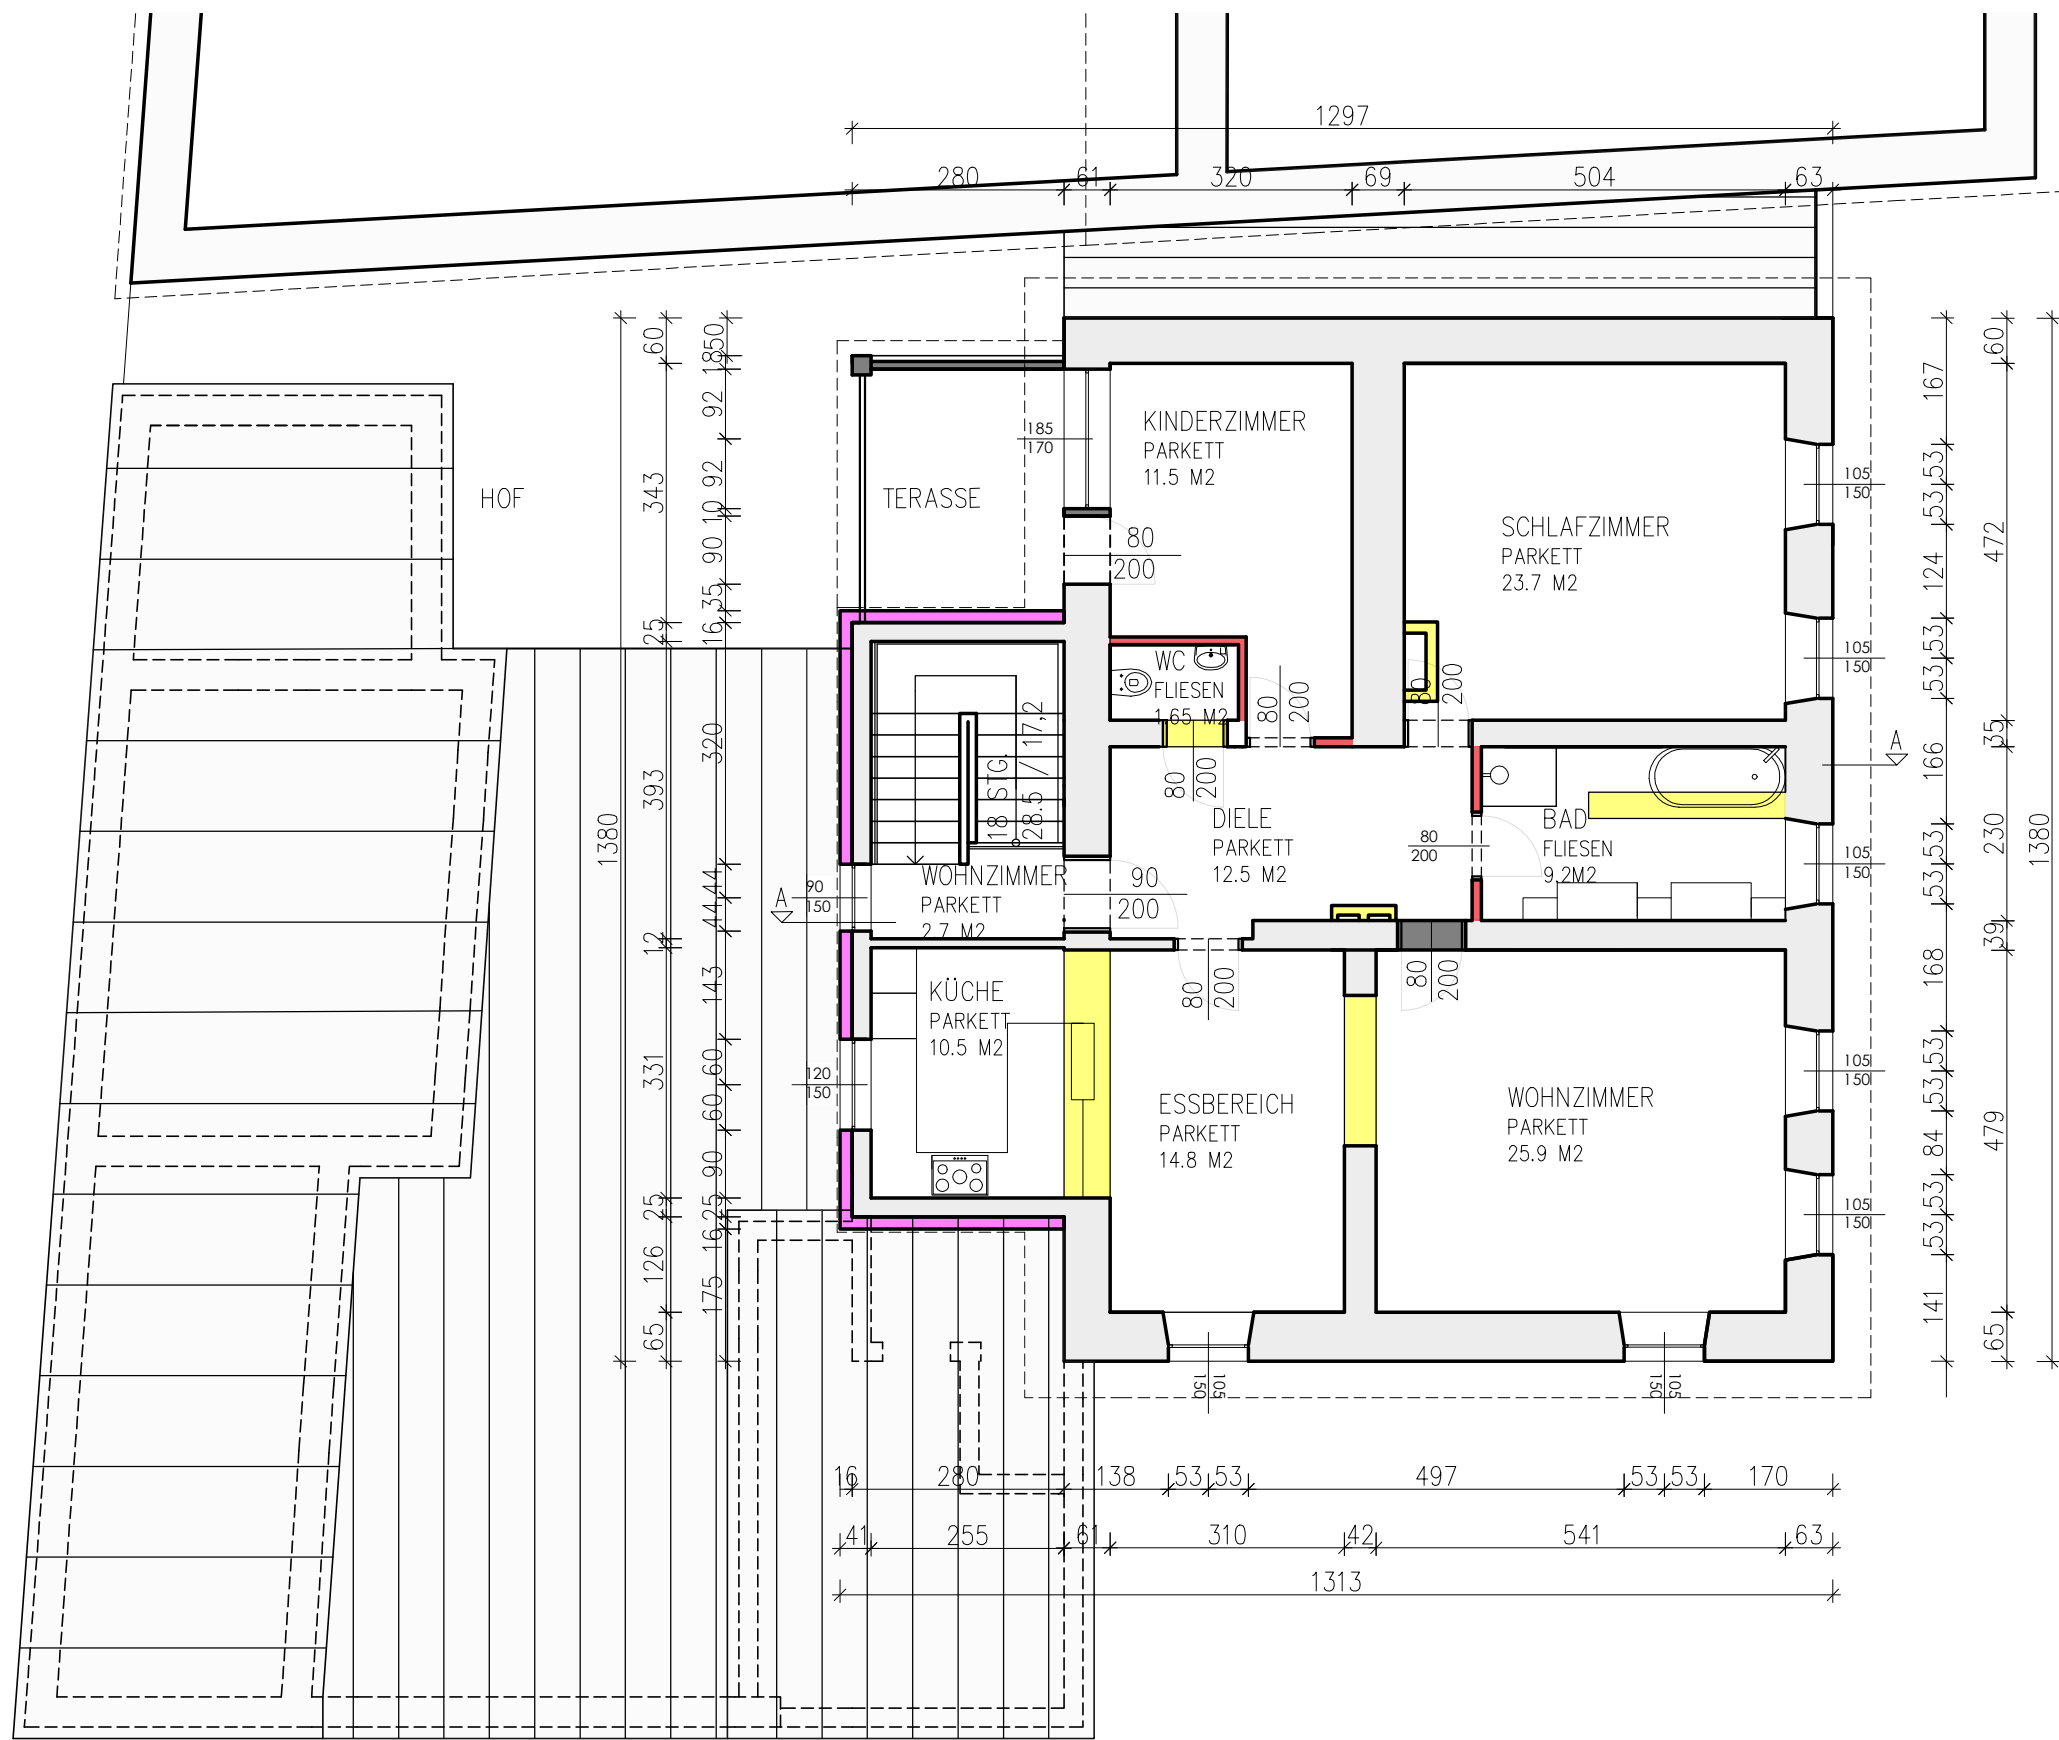


LAGEPLAN

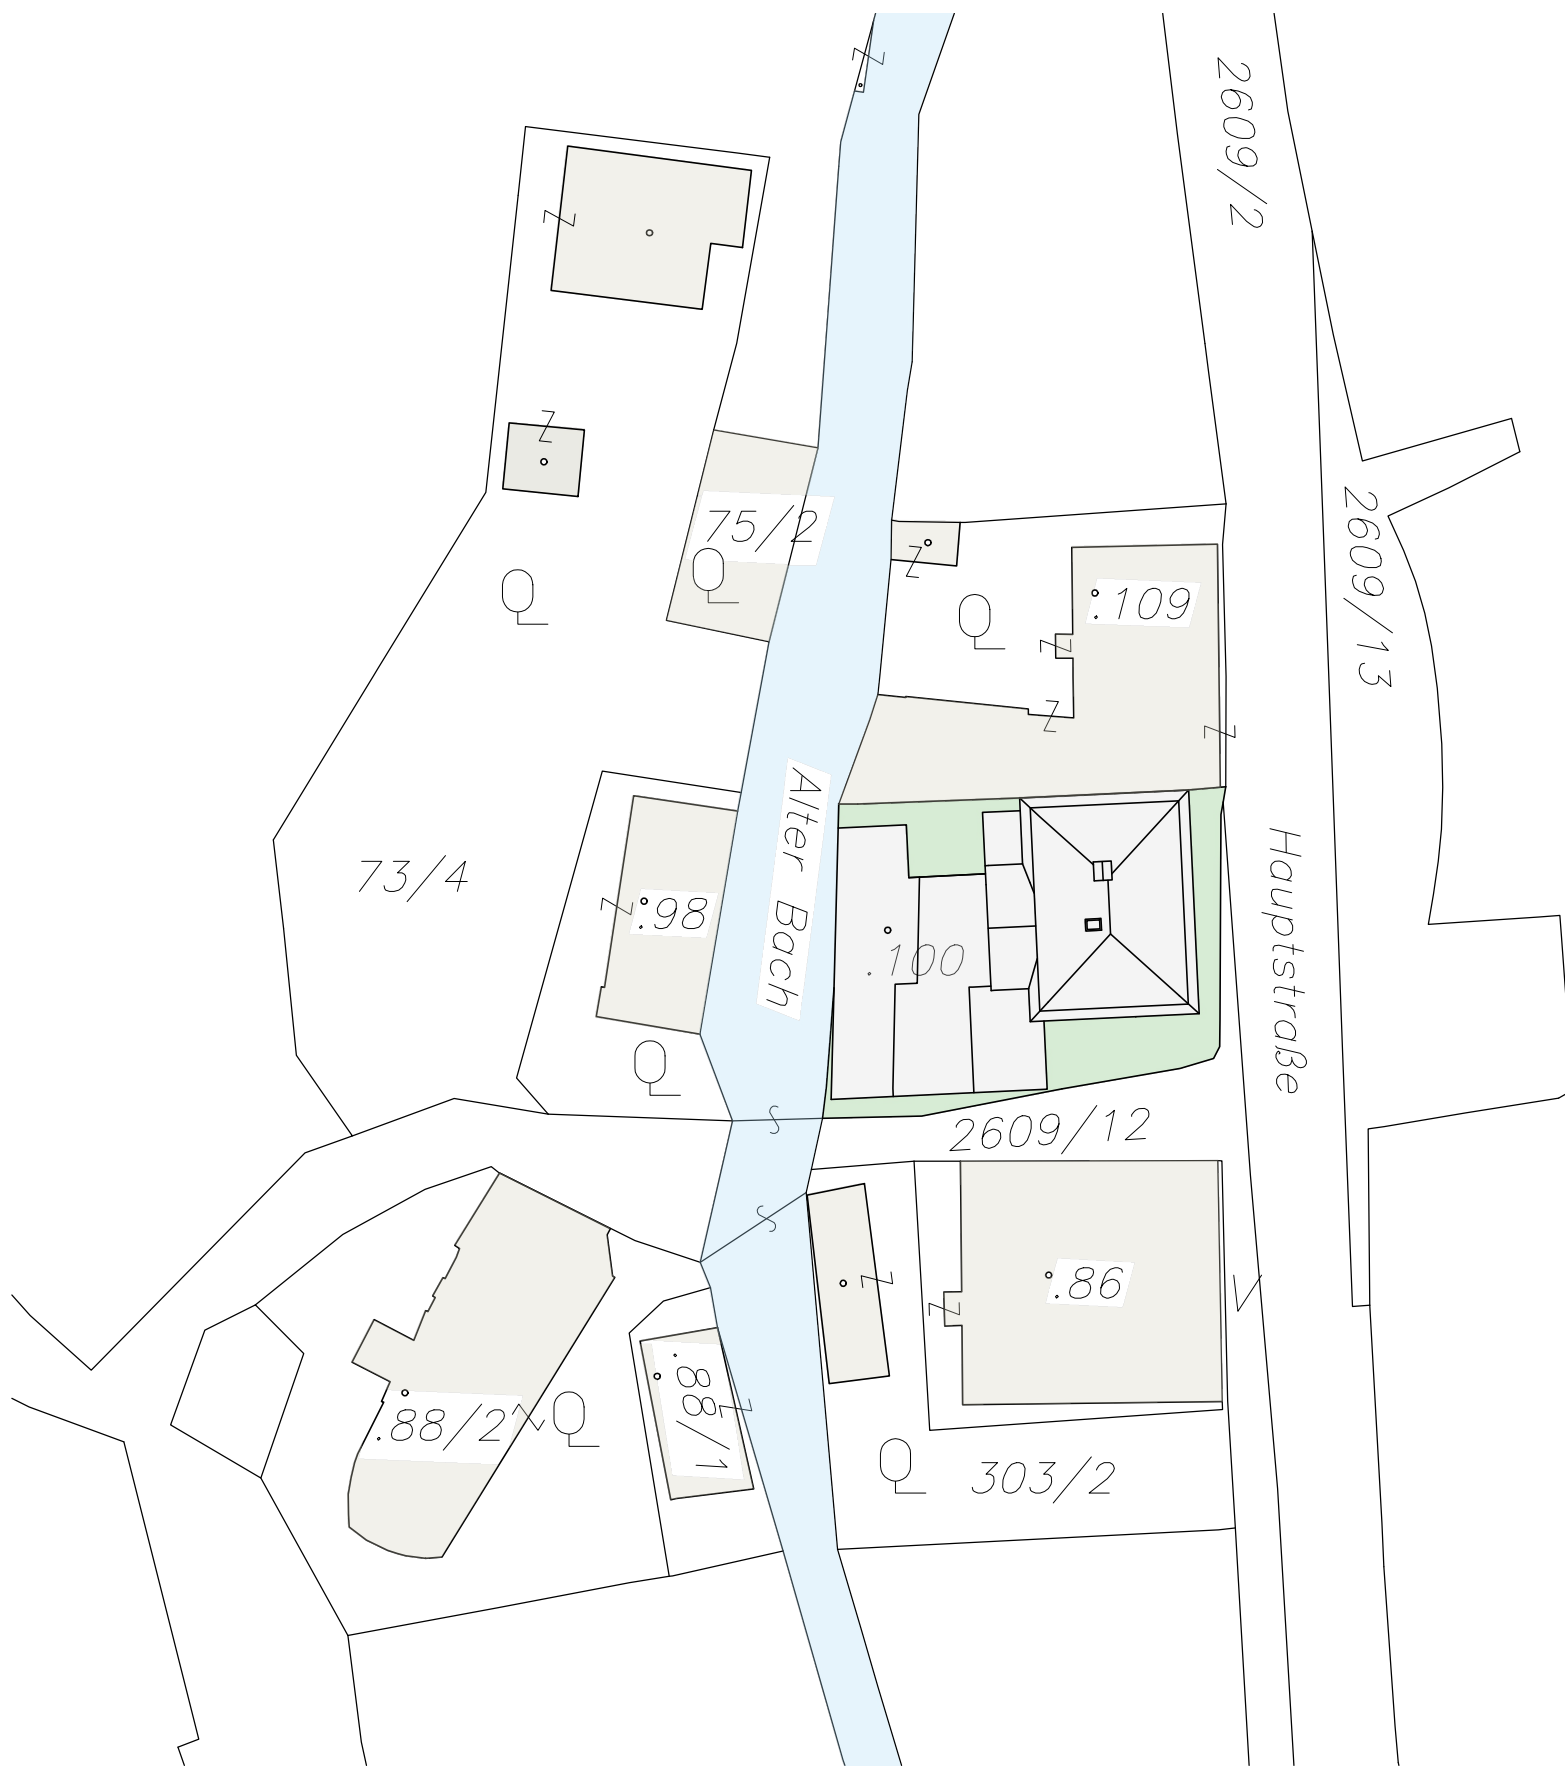

DACHGESCHOSS

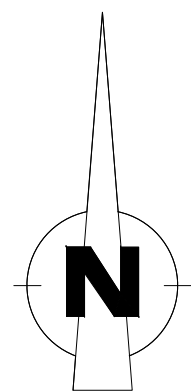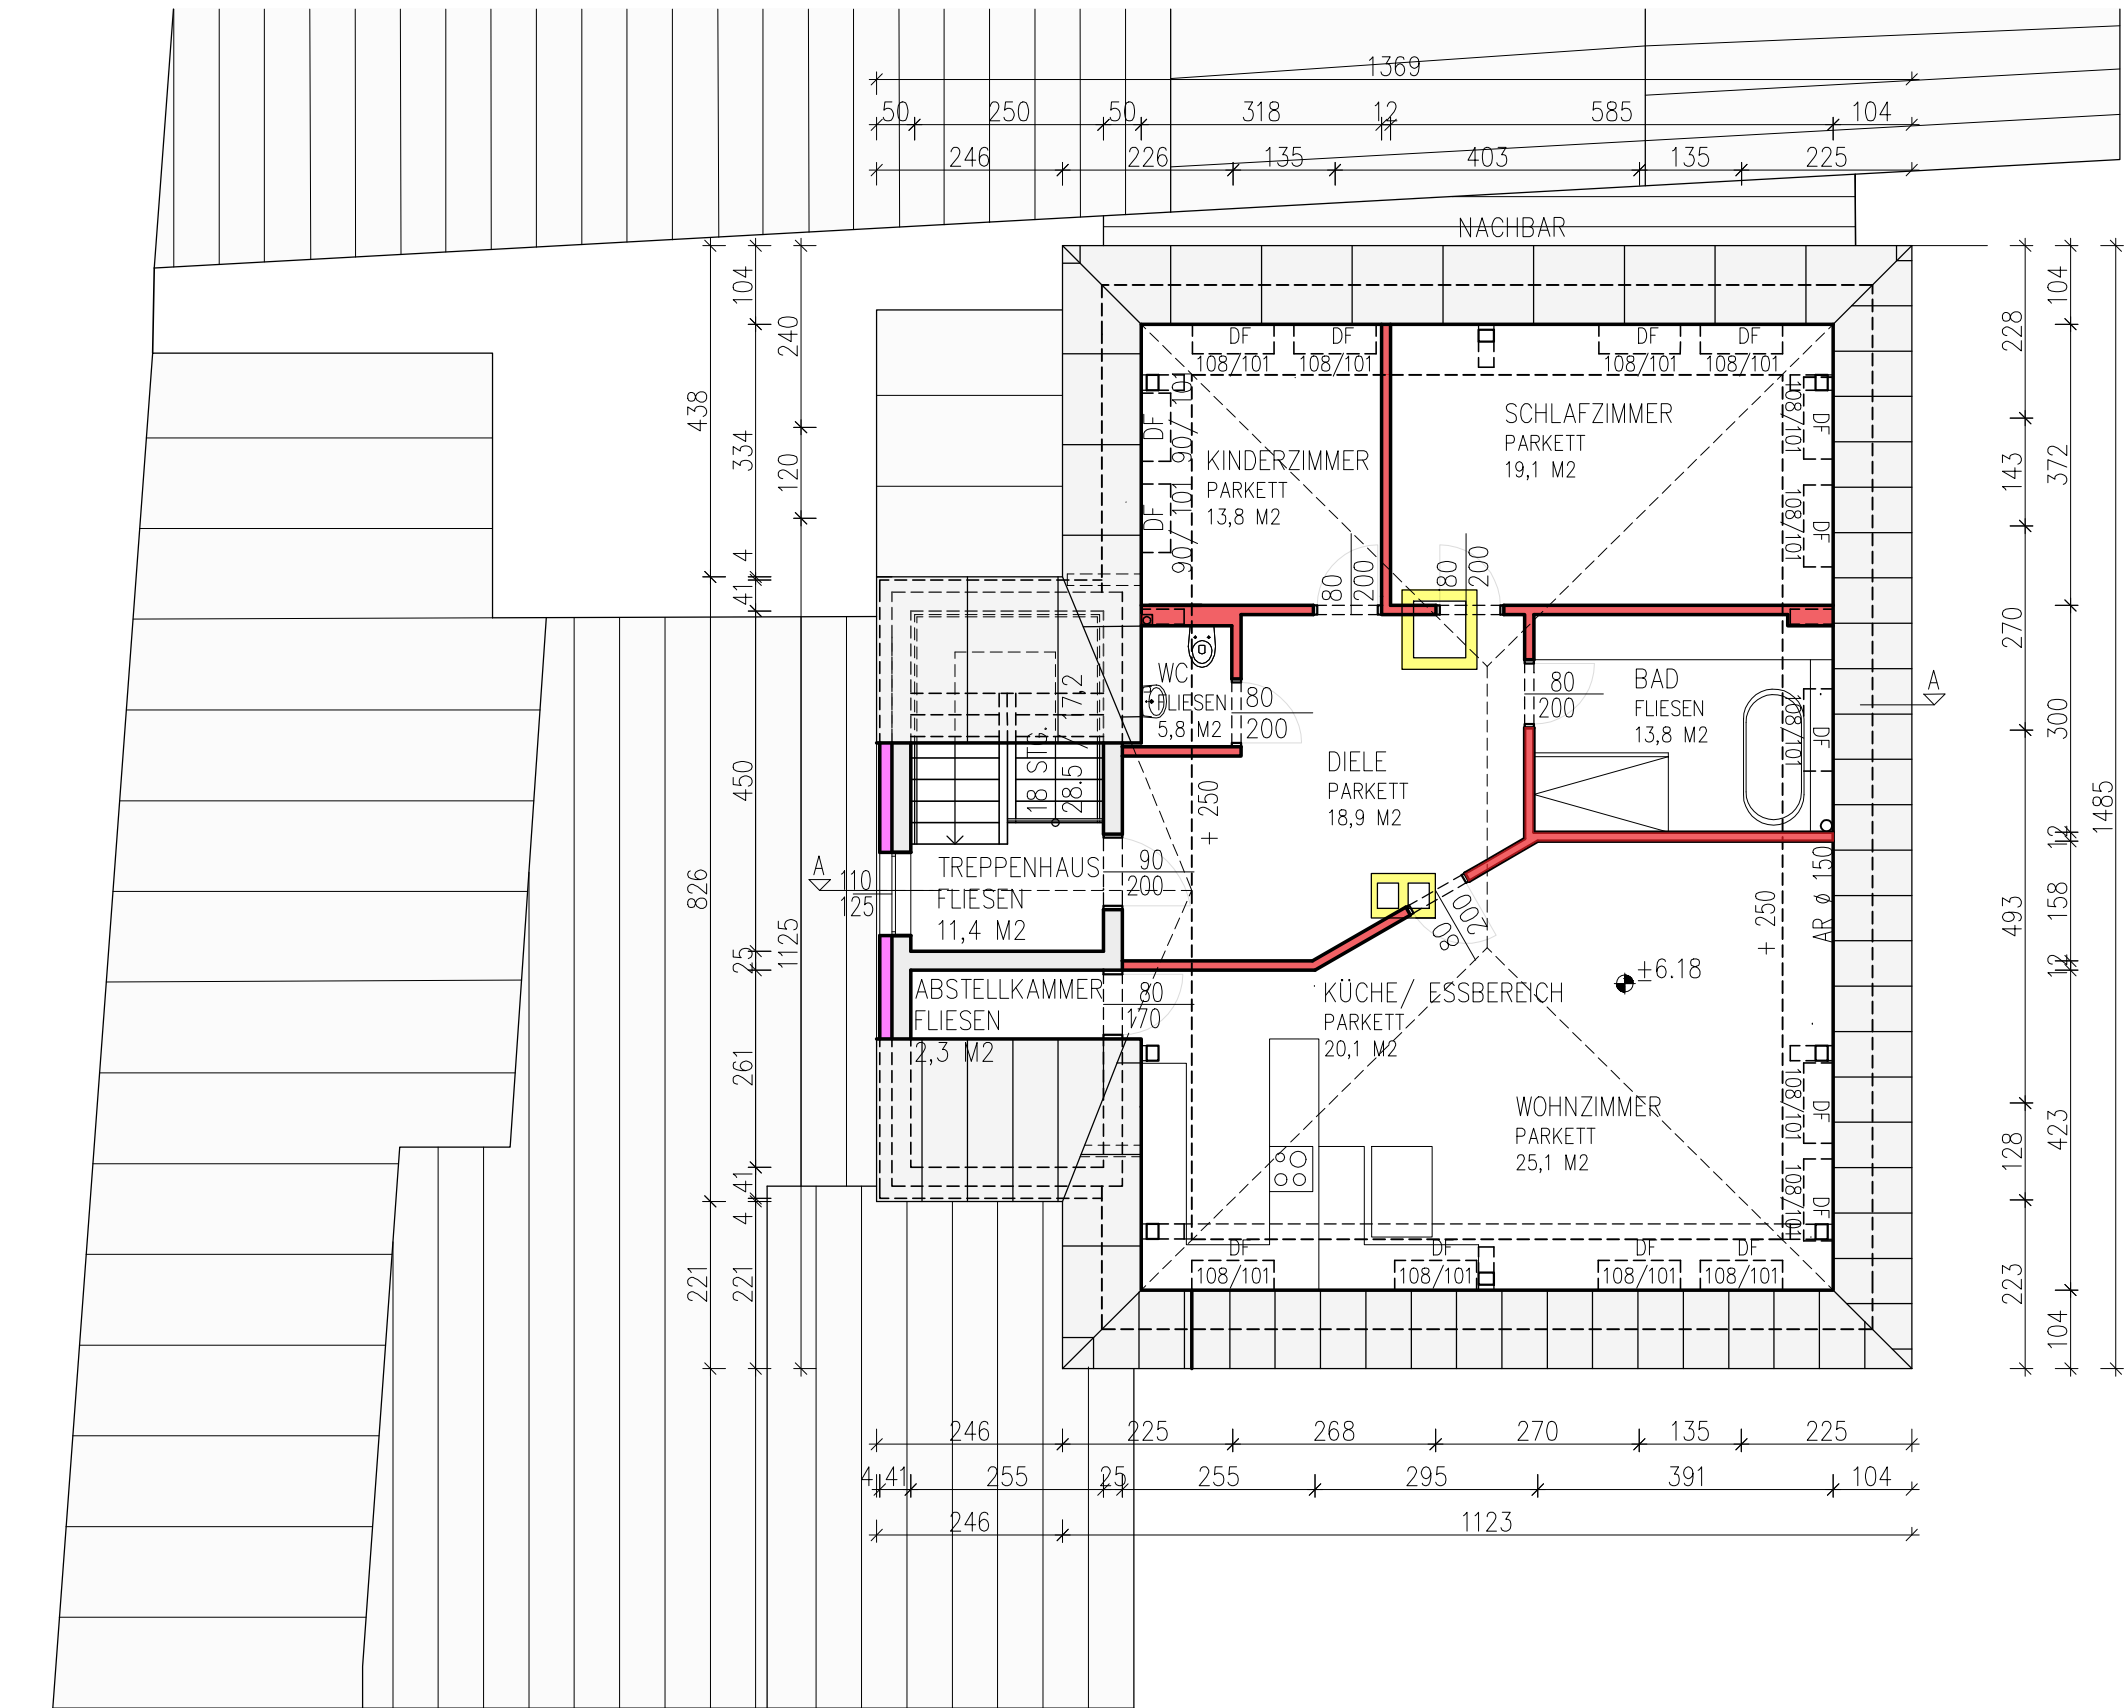


SNITT A-A

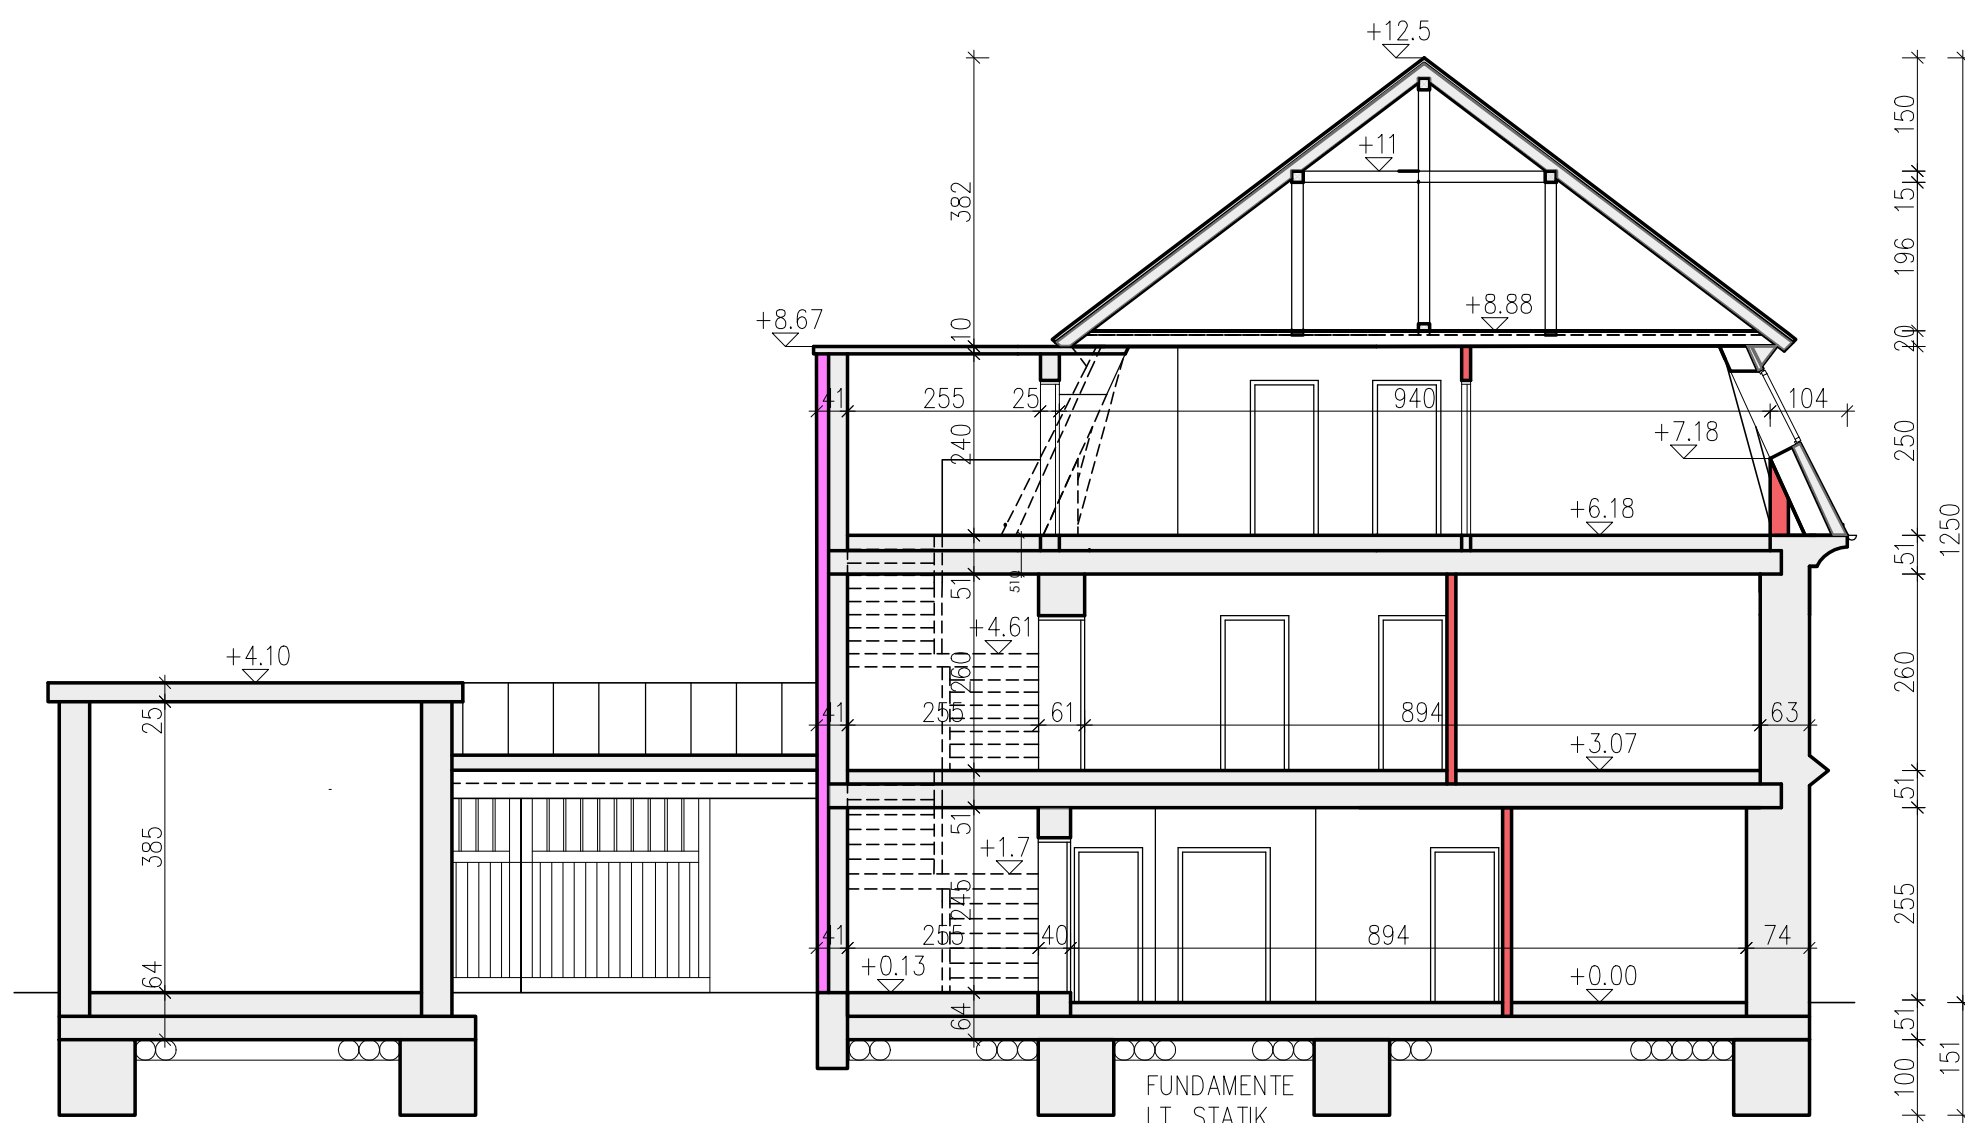

|                                                                                  |                            |                                 |                            |
|----------------------------------------------------------------------------------|----------------------------|---------------------------------|----------------------------|
| <b>EINREICHPLAN</b>                                                              |                            | <b>BESTAND</b><br>ZIEGEL<br>VWS | <b>ABBRUCH</b><br>HOLZ     |
| BAUWERBER<br><b>MAYR EVA UND HANS</b><br>AN DER ZINNE 3<br>4563 MICHELDORF       |                            | BEHÖRDE/VERMERKE                |                            |
| GRUNDEIGENTÜMER<br><b>MAYR EVA UND HANS</b><br>AN DER ZINNE 3<br>4563 MICHELDORF |                            |                                 |                            |
| STATIKER                                                                         |                            |                                 |                            |
| BAUFÜHRER                                                                        |                            |                                 |                            |
| PLANVERFASSER<br>VALENTIN SCHACHINGER<br>MARIE MAIR<br>LEO FELLINGER             |                            |                                 |                            |
| BAUVORHABEN: <b>UMBAUPLANUNG EINFAMILIENHAUS</b><br>AUF GRUNDSTÜCK NR. 100       |                            |                                 |                            |
| SACHE:<br><b>GRUNDRISSSE, SCHNITT A-A, ANSICHTEN</b>                             | MASSTAB:<br><b>1 : 100</b> | DATUM:<br><b>2025-01-08</b>     | PLAN-NUMMER:<br><b>E 2</b> |
| LAGEPLAN                                                                         |                            | 1 : 500                         |                            |

ANSICHT OST

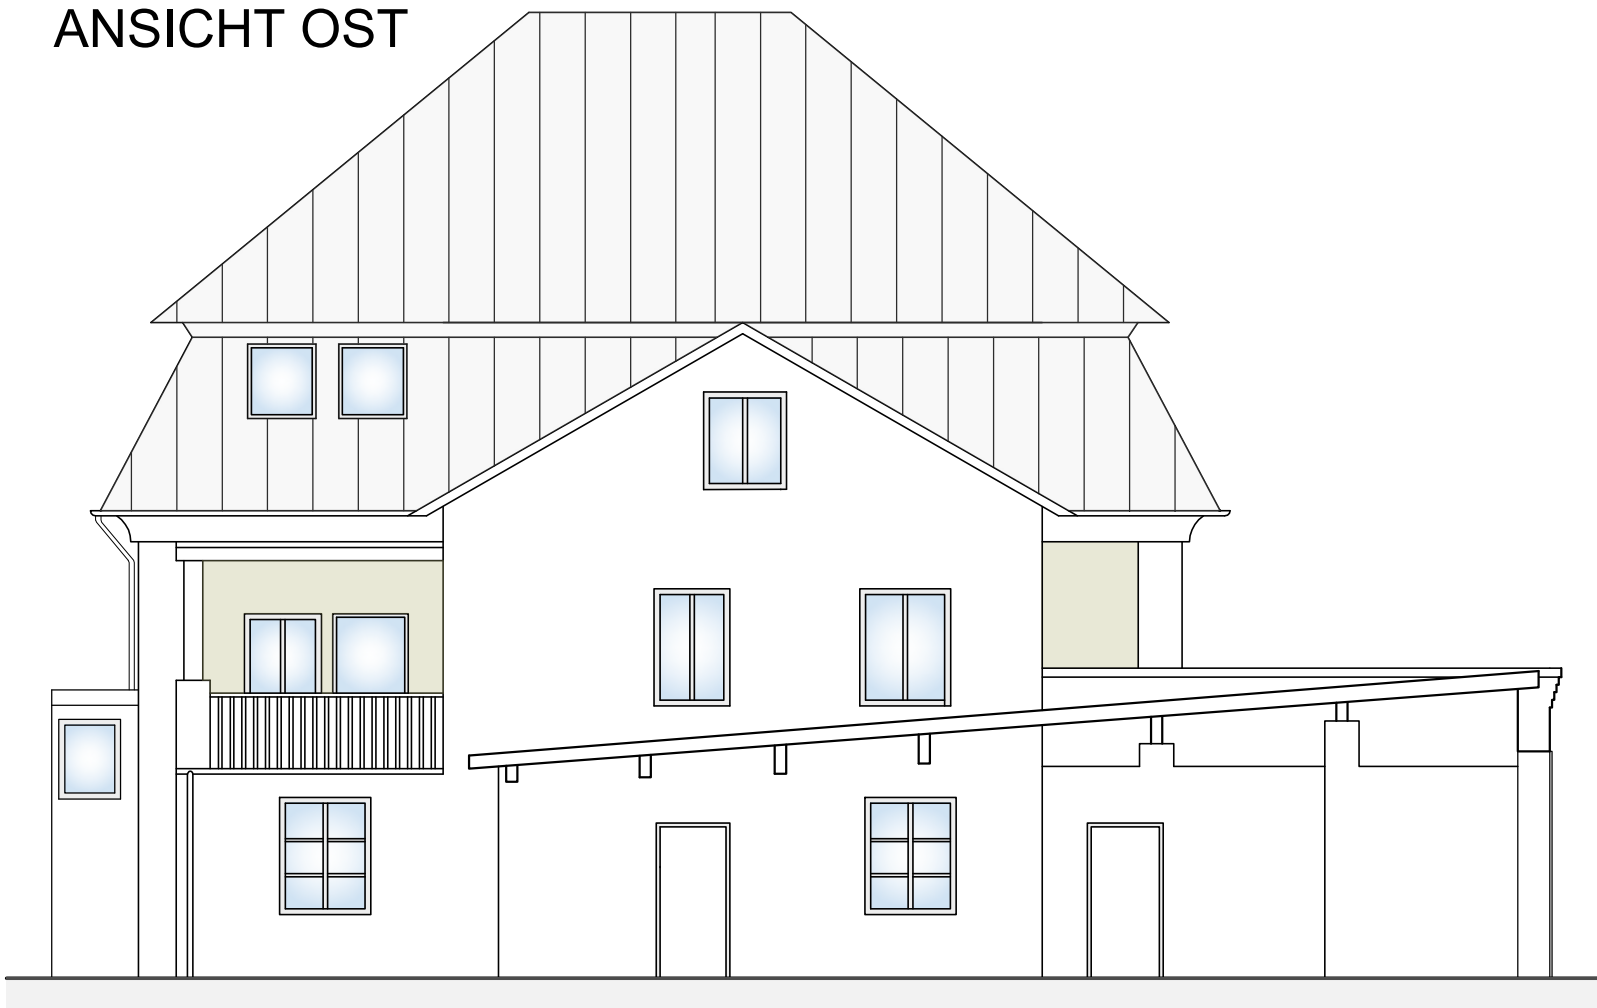

ANSICHT NORD



ANSICHT WEST



ANSICHT SÜD



# EINREICHPLAN

BESTAND  
ZIEGEL

ABBRUCH

HOLZ

BAUWERBER

MAYR EVA UND HANS  
AN DER ZINNE 3  
4563 MICHELDORF

GRUNDEIGENTÜMER

MAYR EVA UND HANS  
AN DER ZINNE 3  
4563 MICHELDORF

STATIKER

BAUFÜHRER

PLANVERFASSEN  
VALENTIN SCHACHINGER  
MARIE MAIR  
LEO FELLINGER

BEHÖRDE/VERMERKE

BAUVORHABEN: **UMBAUPLANUNG EINFAMILIENHAUS**

AUF GRUNDSTÜCK NR. 100

SACHE: **GRUNDRISSSE, SCHNITT A-A, ANSICHTEN**

MASSTAB:  
**1 : 100**

DATUM:  
**2025-01-08**

PLAN-NUMMER:  
**E 1**

LAGEPLAN

1 : 500