



GRUNDRISS DACHGESCHOSS M 1:50

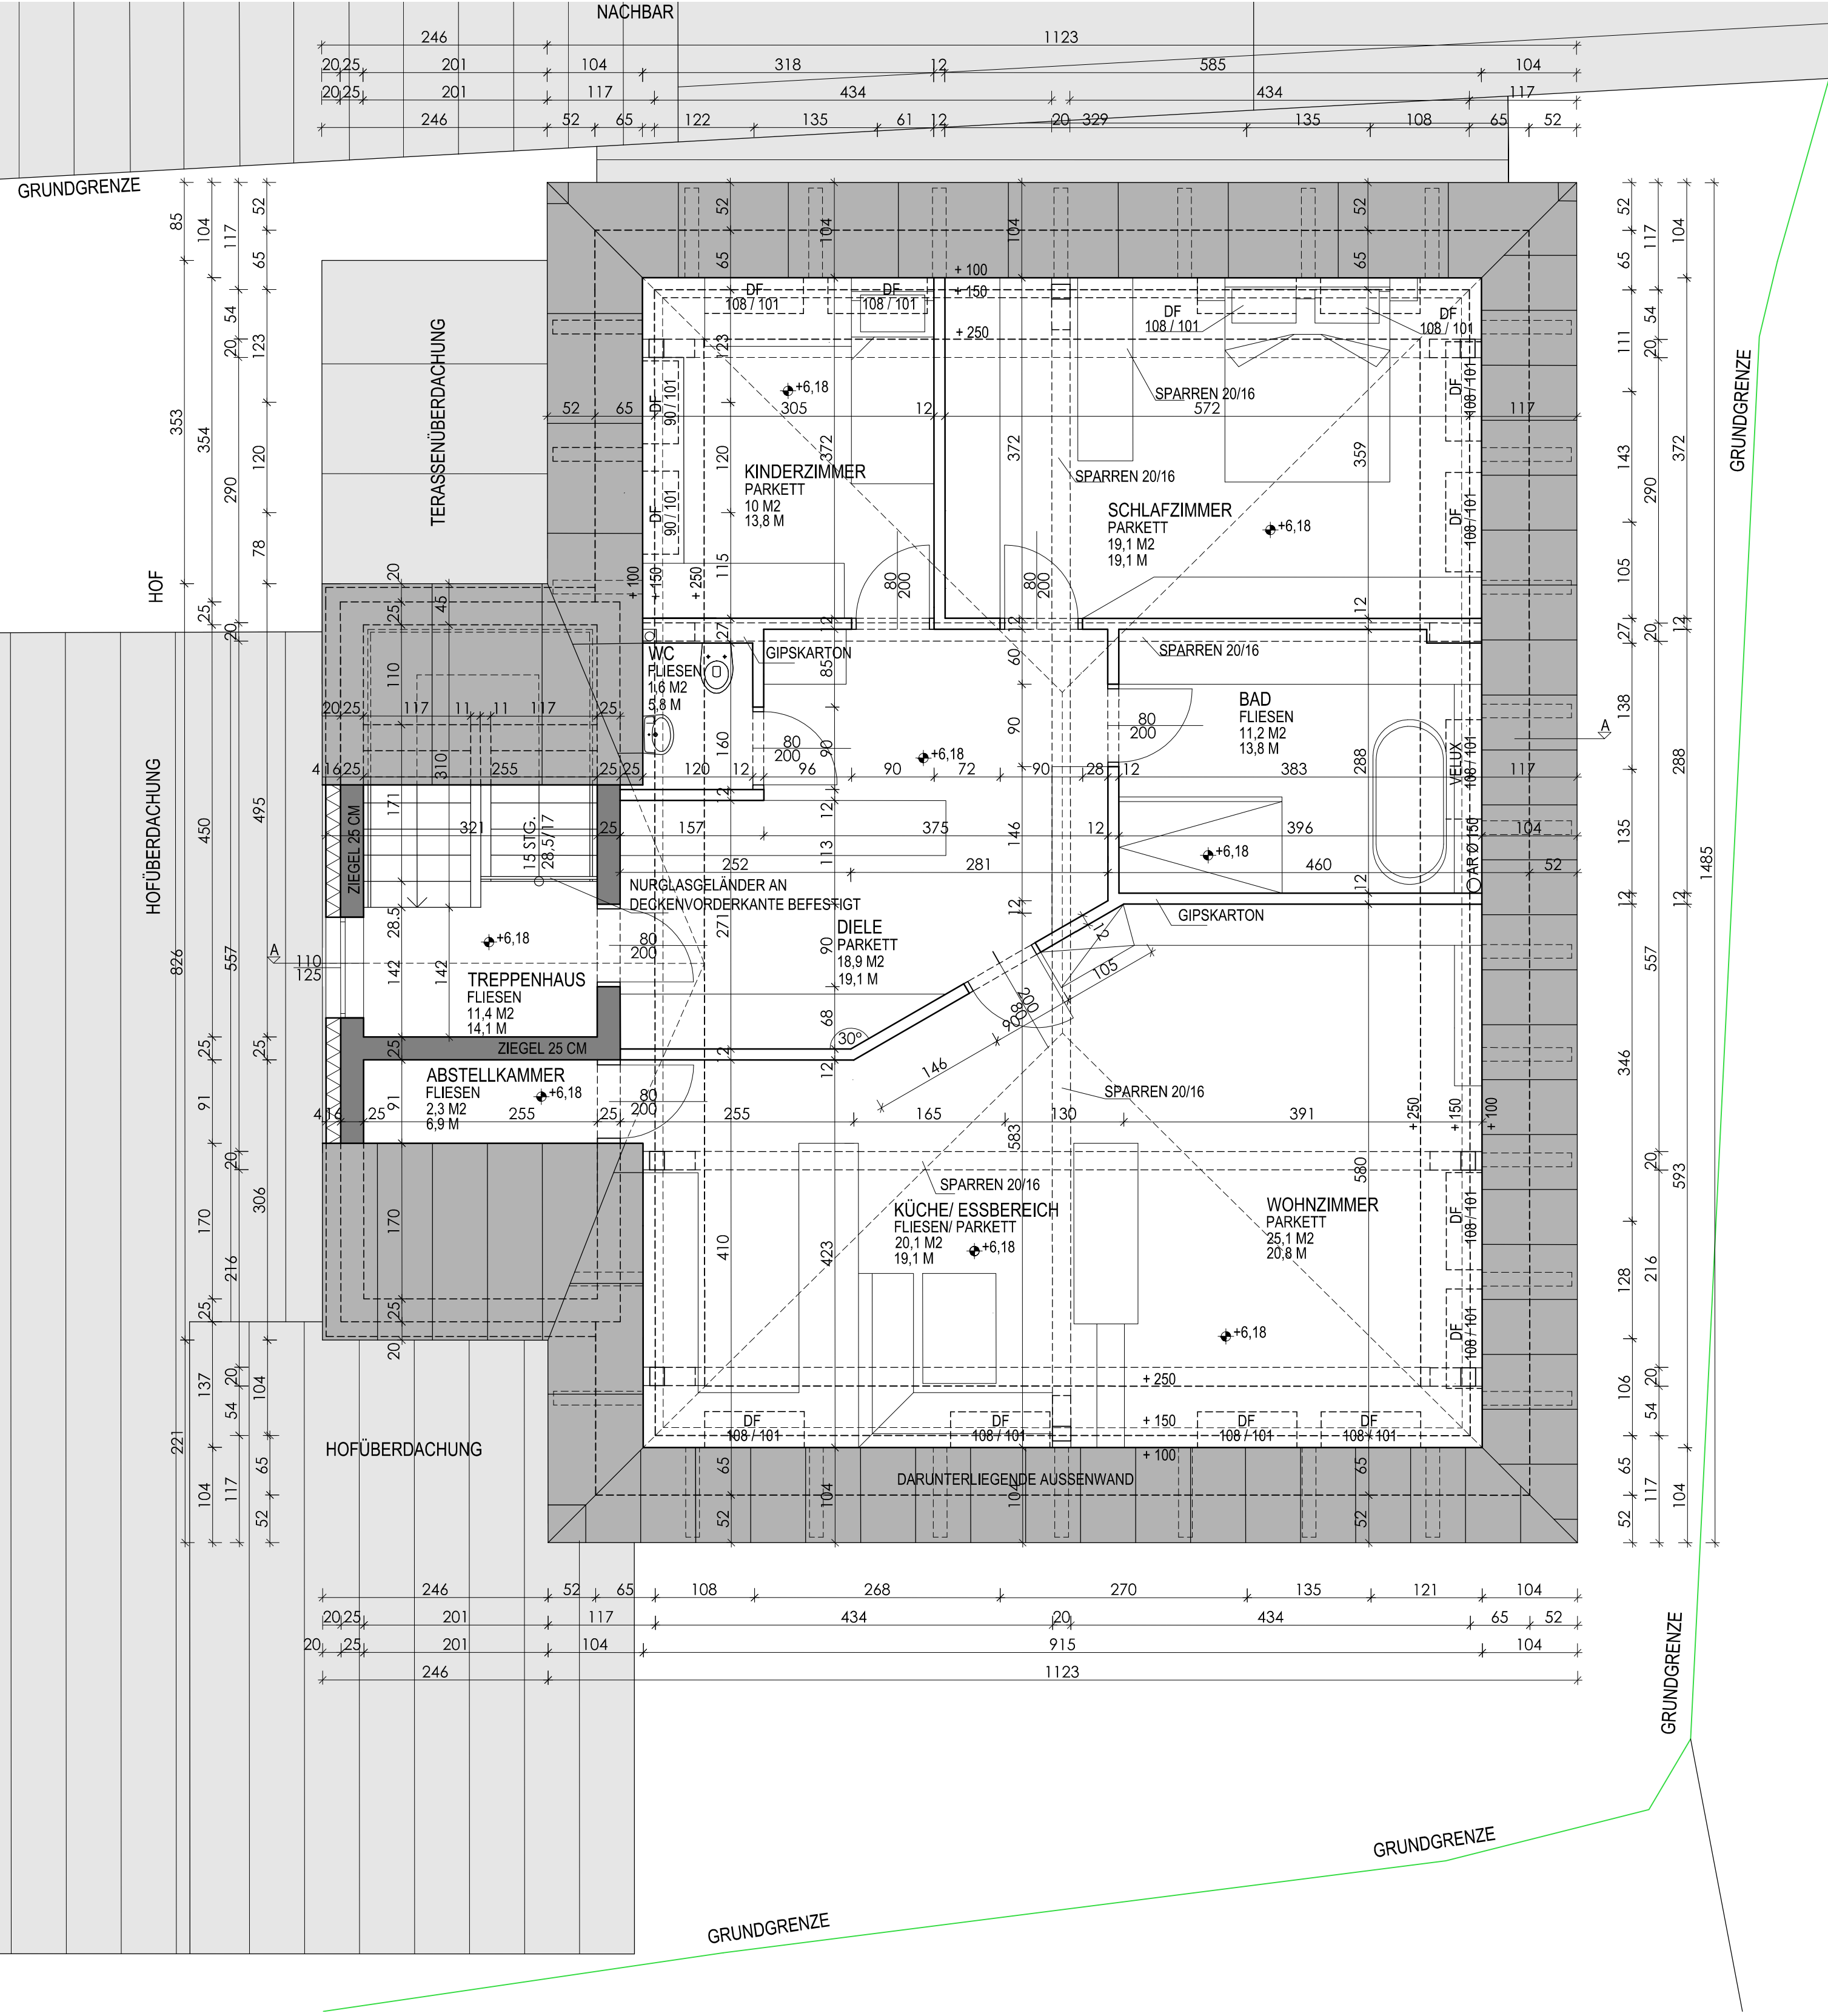

SCHNITT A-A DACHGESCHOSS M 1:50

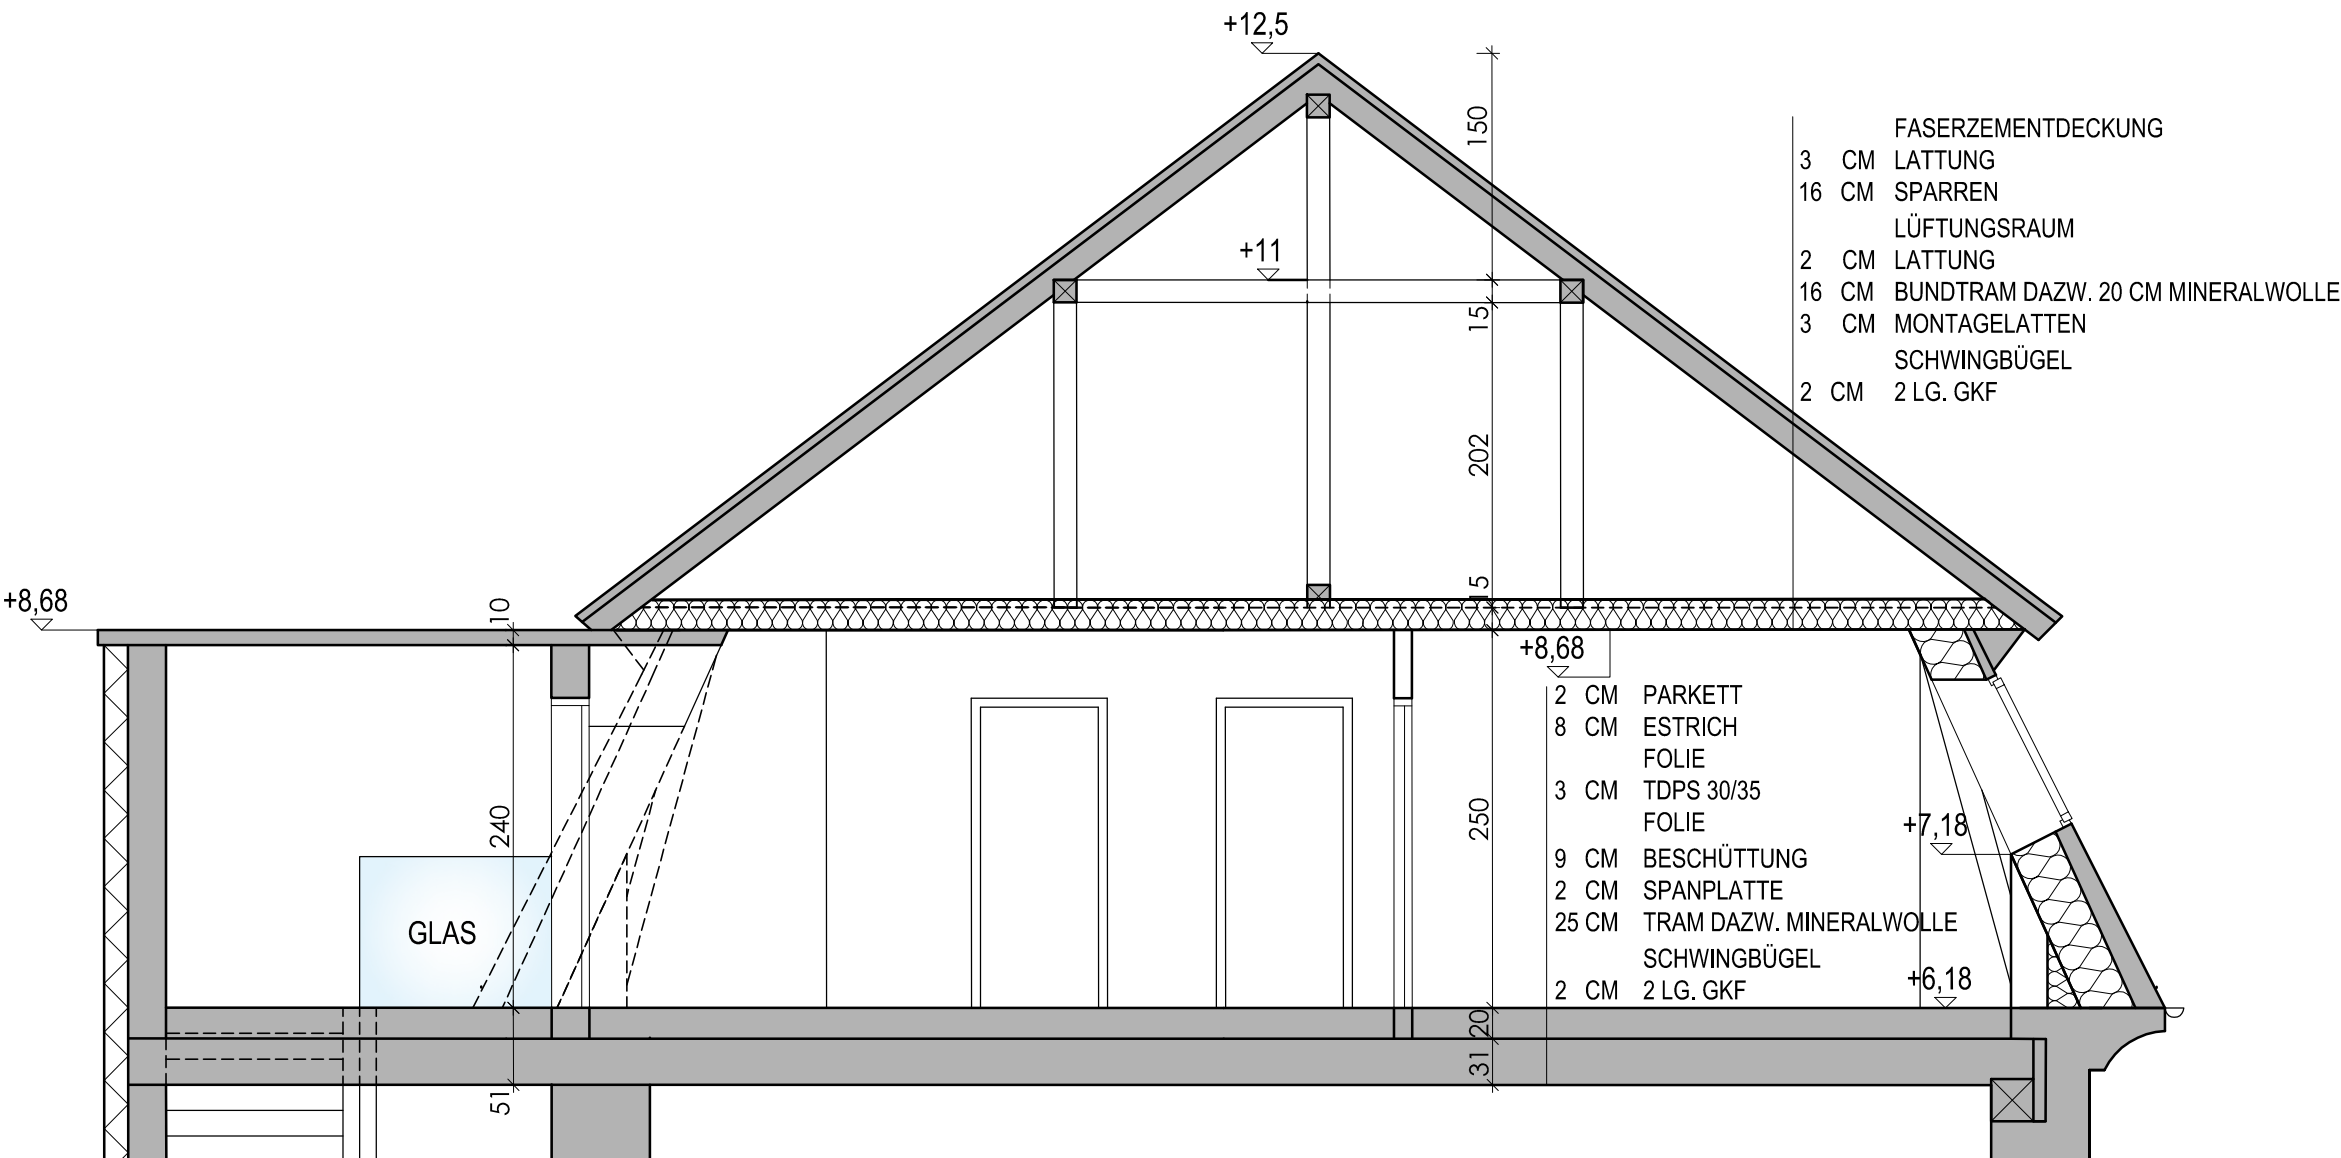

LEGENDE:

- KANAL
- BEZUGSLINIE
- PS PUTZSCHACHT
- AR ABFALLROHR
- RR REGENROHR
- ML MAUERLICHTE
AB OBERKANTE FERTIGER FUSSBODEN
- DVK DECKENVORDERKANTE
- SI SICKERSCHACHT
- STÄHLBETON
- STAHL
- GIPSKARTONWAND
- BESTAND
- WÄRMEDÄMMUNG - VWS

POLIERPLAN

NATURMASSE NEHMEN
KOTEN PRÜFEN
UNSTIMMIGKEITEN SIND MIT
DER ÖRTLICHEN BAUAUFSICHT
ZU KLÄREN

BAUHERR: JOHANNES MAYER UND EVA MAYER
HAUPTSTRASSE 28, 4563 MICHELDORF

BAUVORHABEN: WOHN-EINHEITEN

AUF GRUNDSTÜCK NR. 2609/12 EZ. 100 KG.: 4563 MICHELDORF

SACHE: DACHGESCHOSS

MAßSTAB: 1:50

GEZ.:	NAME:	DATUM:	GEÄ.:	NAME:	DATUM:
GEÄ.:	SCHACHINGER	11.12.2024	GEÄ.:		
GEÄ.:			GEÄ.:		
GEÄ.:			GEÄ.:		

PLAN-NUMMER:

P1