




GRUNDRISS DACHGESCHOSS M 1:50

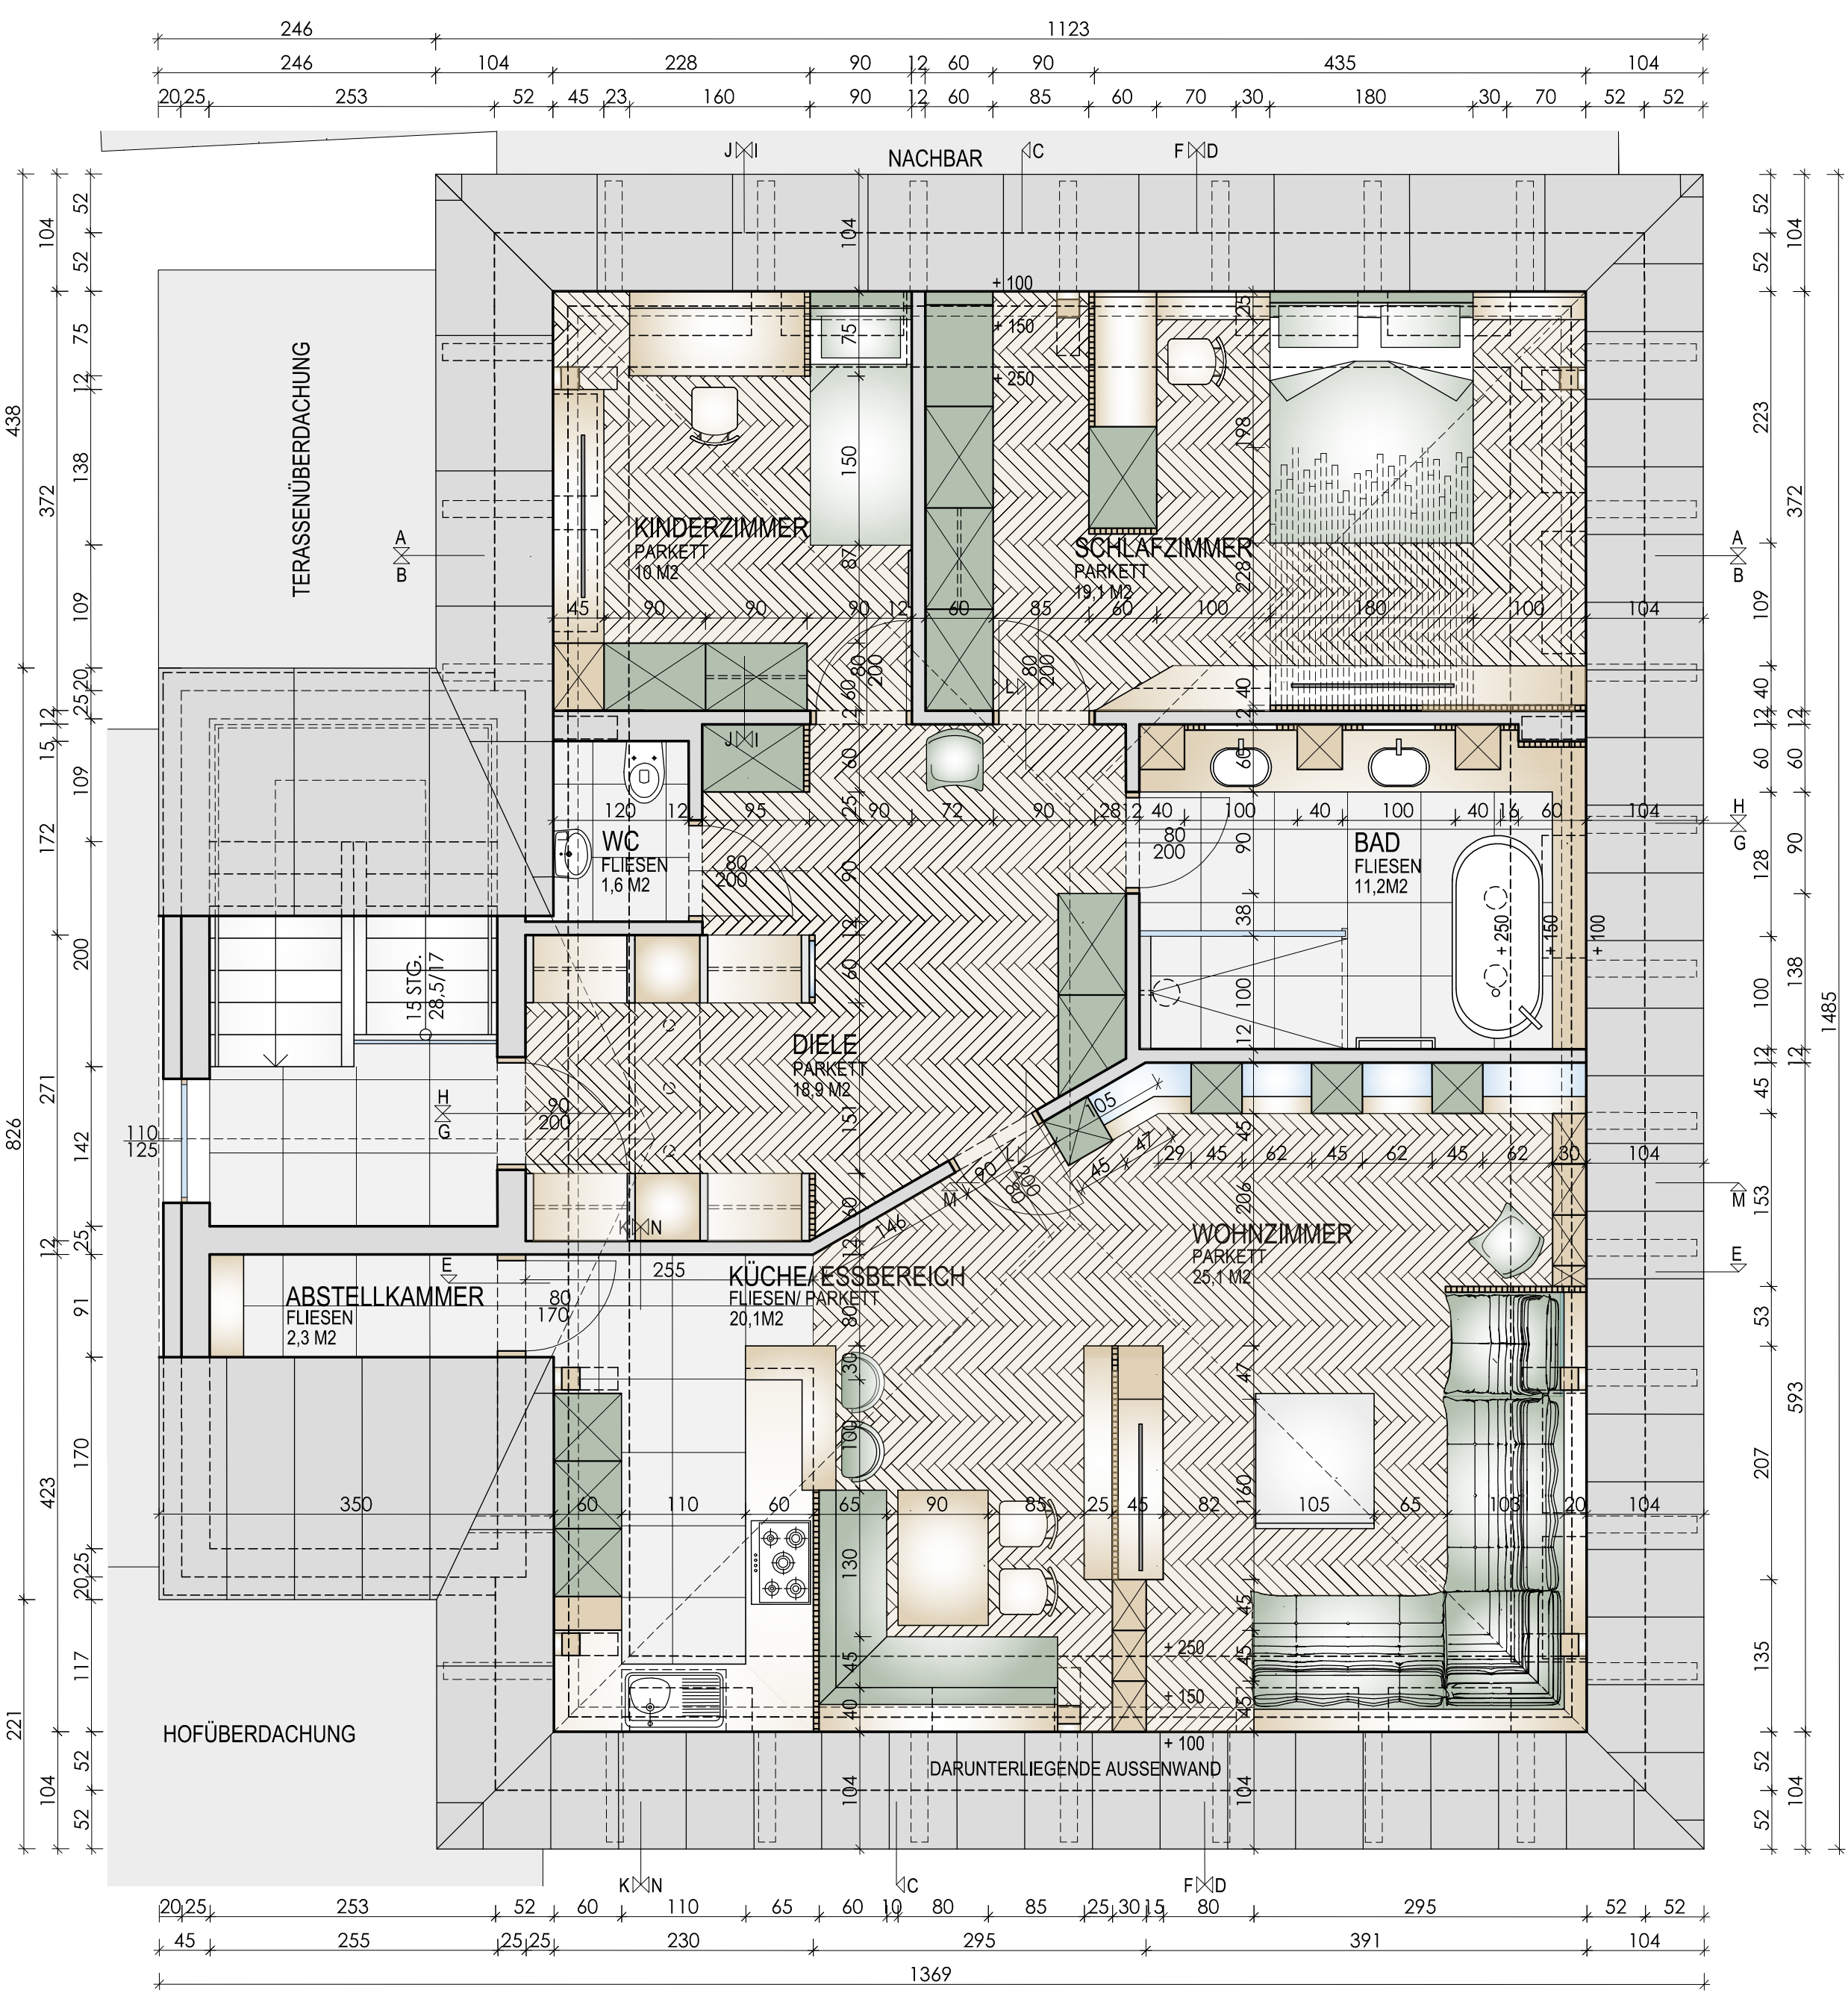


ANSICHT D - D M 1:50

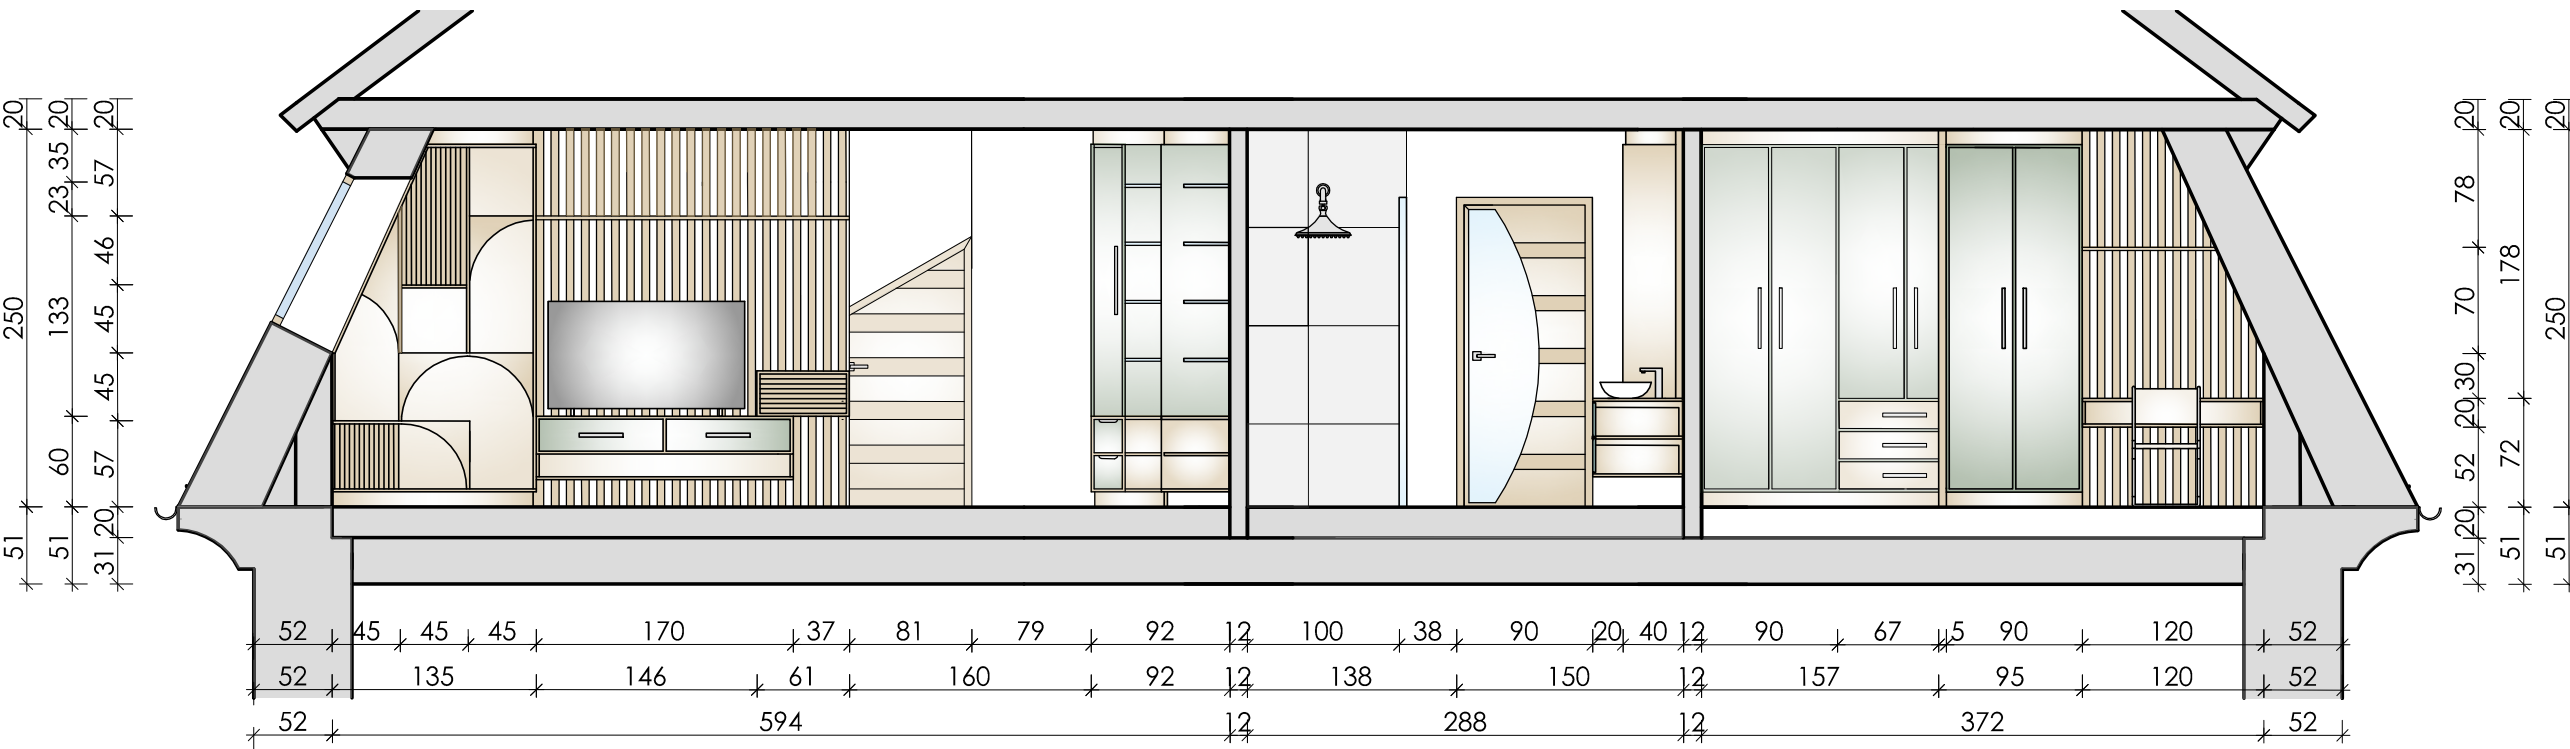


ANSICHT A - A M 1:50

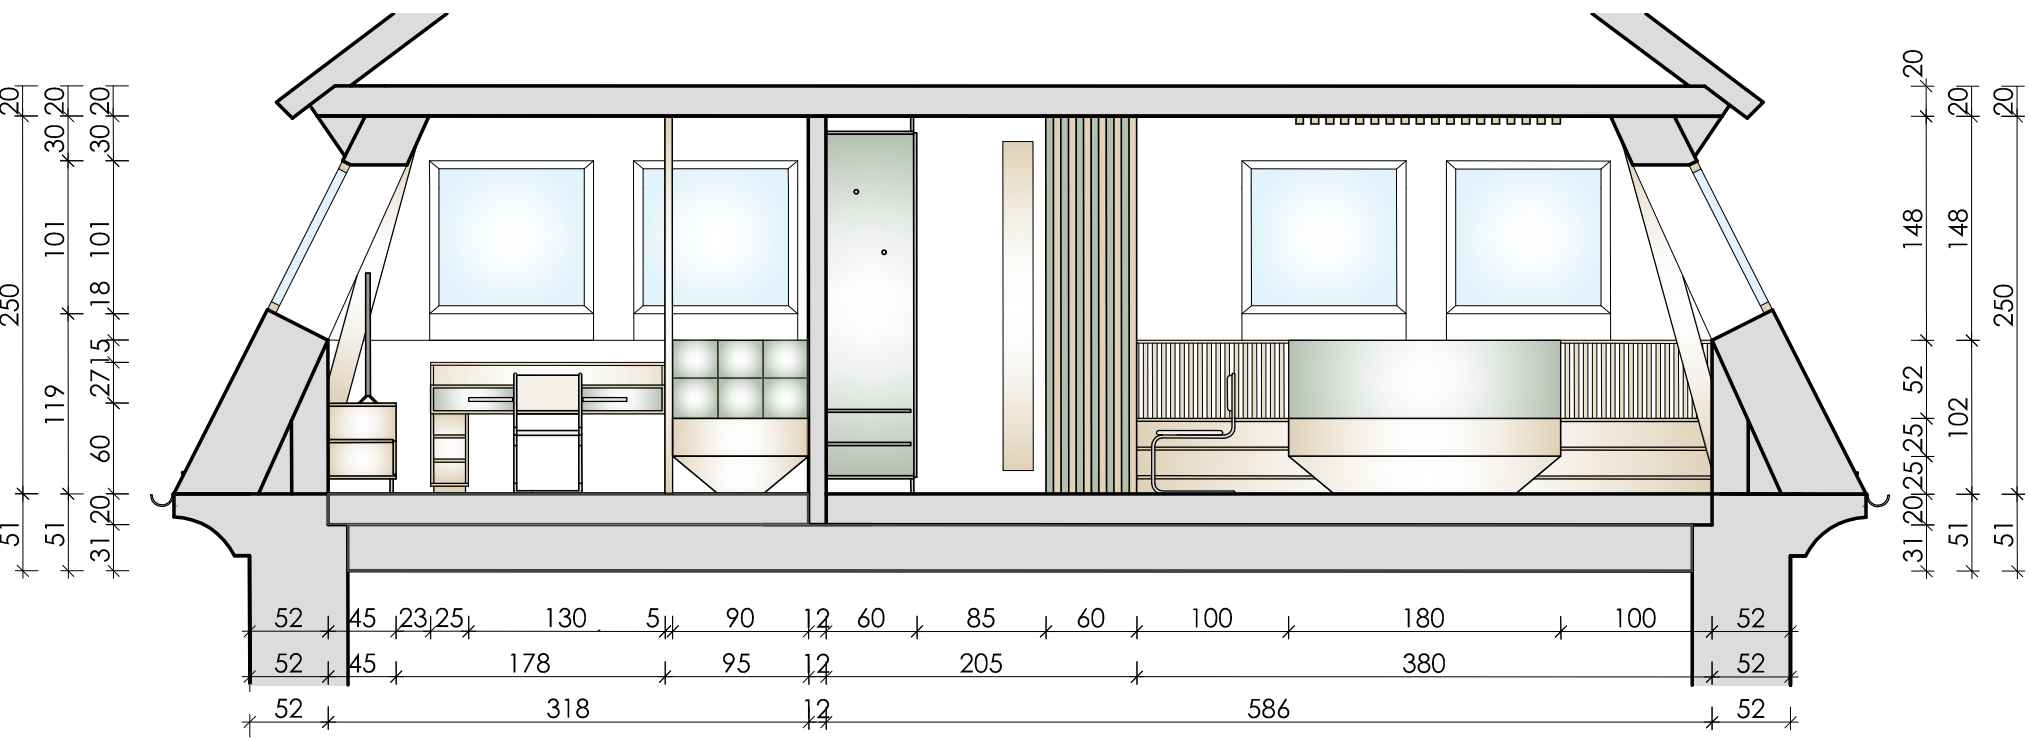


ANSICHT I - I M 1:50

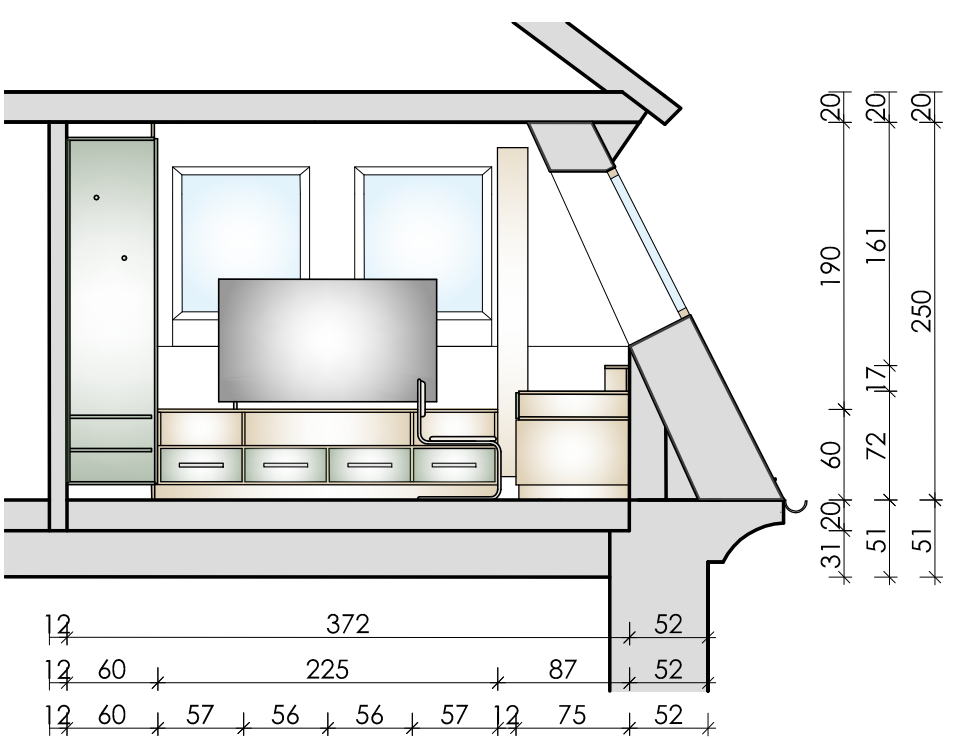


ANSICHT B - B M 1:50

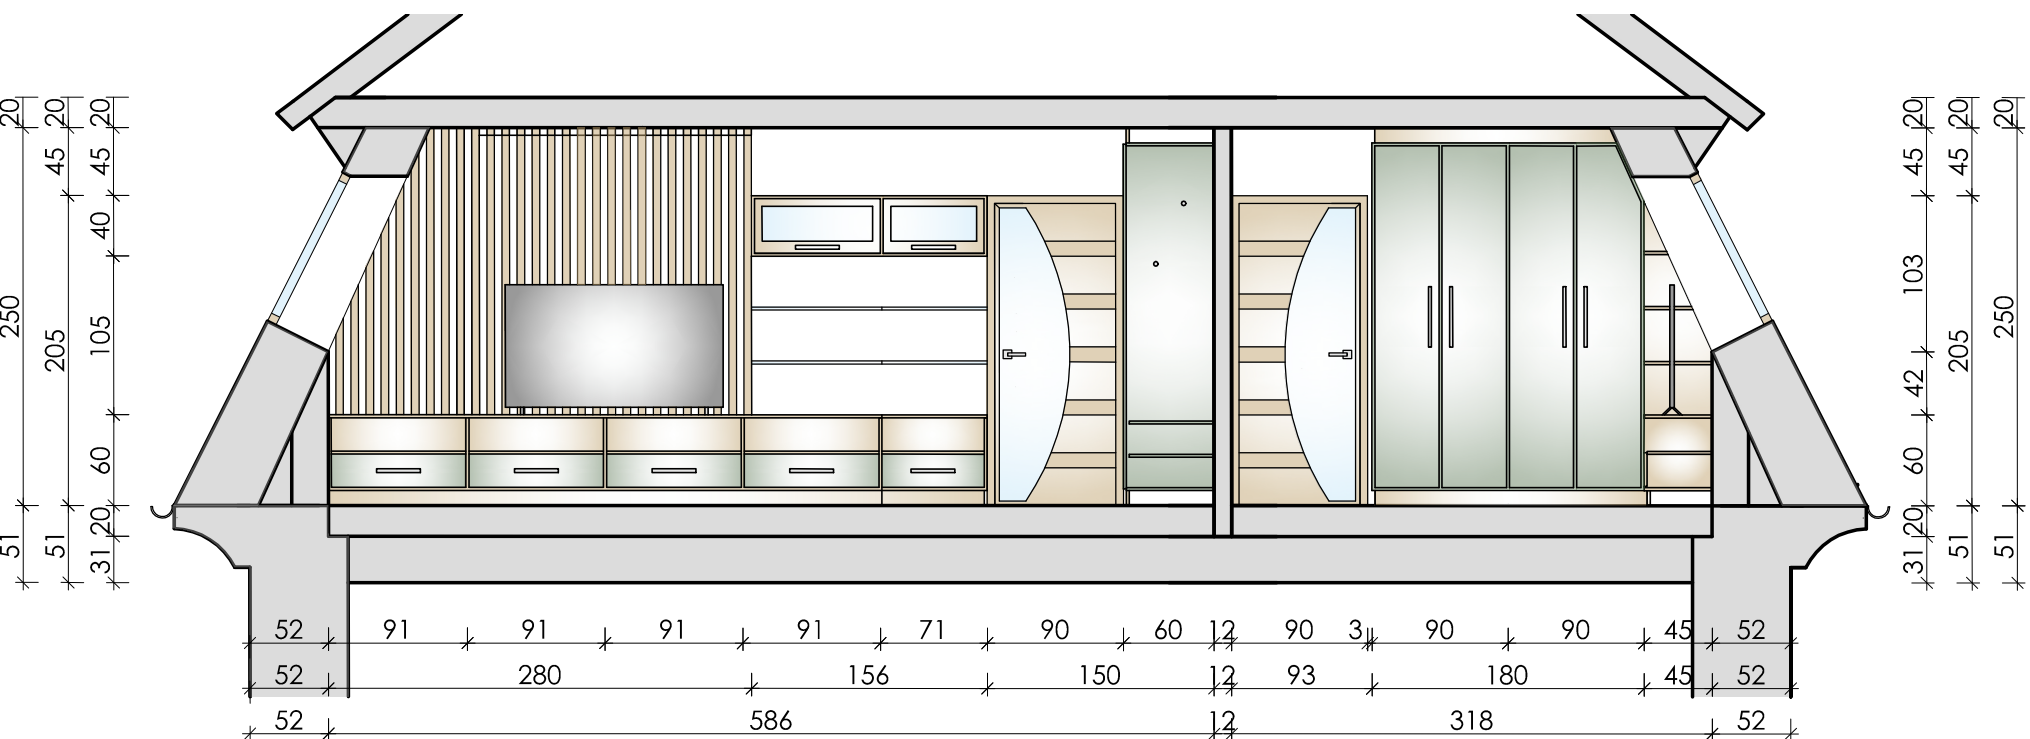

ANSICHT J - J M 1:50

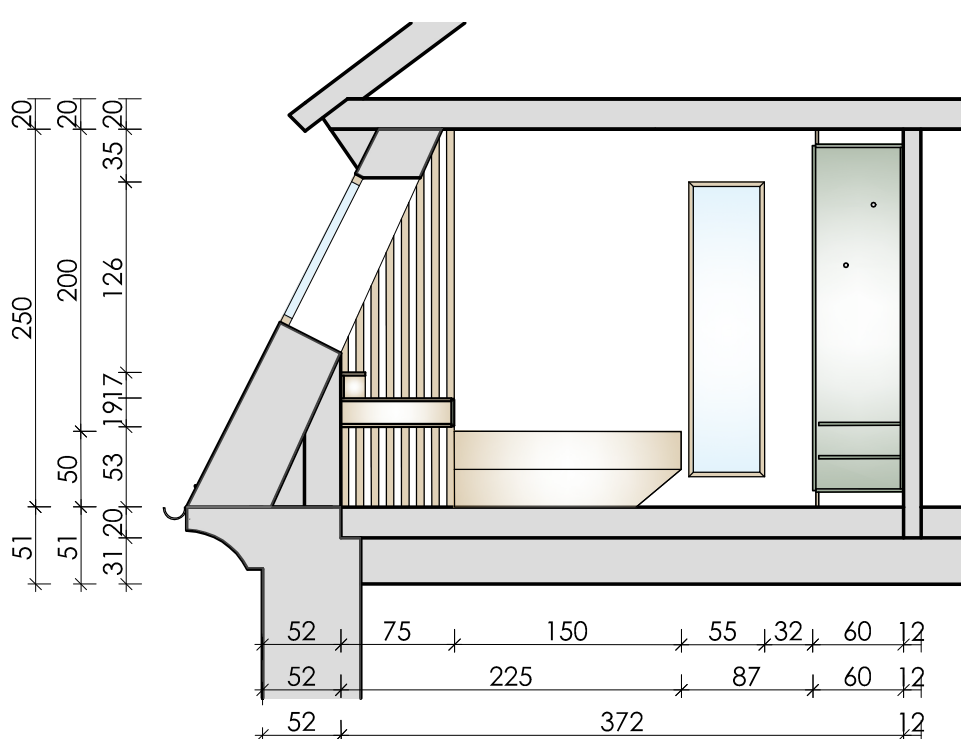

ANSICHT C - C M 1:50

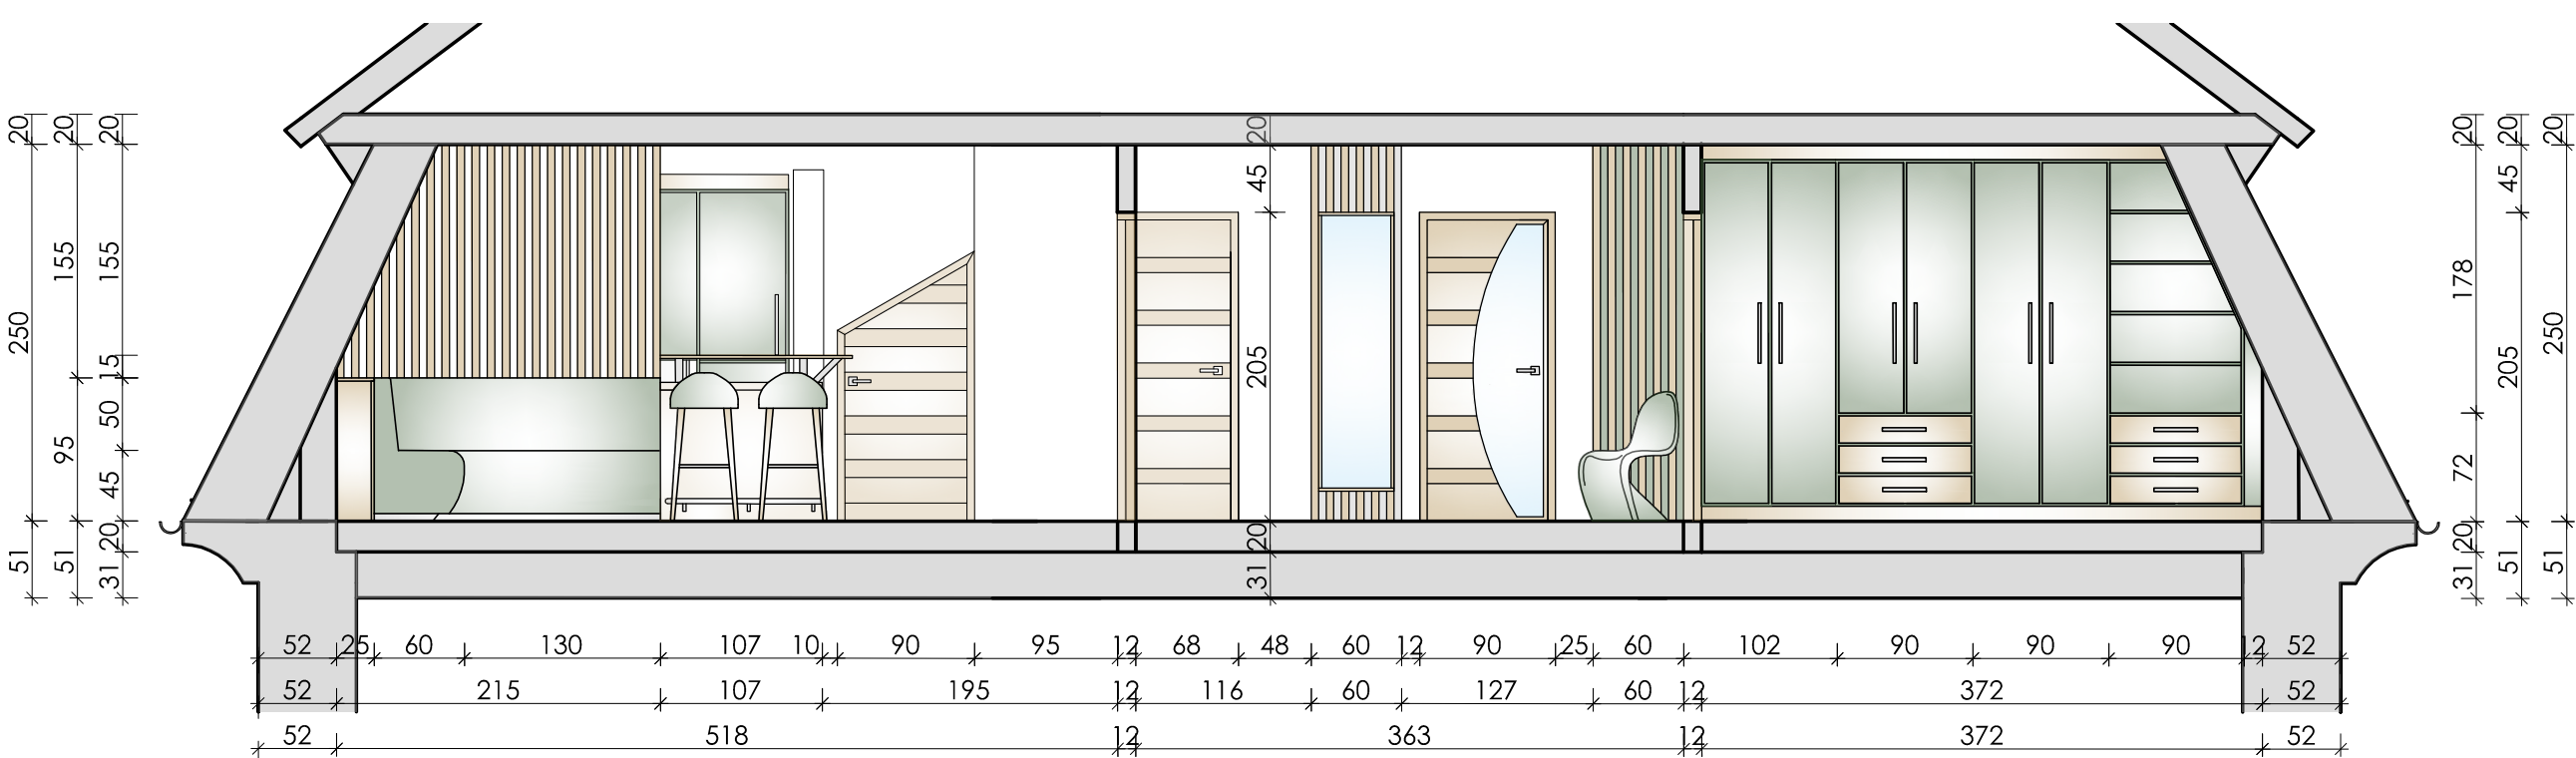

ANSICHT F - F M 1:50

